

8/5/2024 8:05:08 PM

THIS DRAWING AND THE INFORMATION CONTAINED HEREIN ARE THE COPYRIGHTED WORK OF OMGIVNING ARCHITECTS AND MAY NOT BE REPRODUCED WITHOUT WRITTEN PERMISSION.



1ST FLOOR UPPER PLAN
1" = 20'-0"

LEGEND

- WALL
- AREA NOT A PART
- (E) TENANT NOT A PART

Plans Approved
as required by
City Los Angeles
Zoning Administrator
ZA-2017-5013-MCUP
Case No.
Ricardo Martinez
Signature
09/17/2024
Date

OMGIVNING
architecture / interiors

1301 N. BROADWAY
LOS ANGELES, CA 90012

EL CENTRO
6200 HOLLYWOOD BLVD.
LOS ANGELES, CA 90028


CUP/CUB PLAN

REVISIONS:

08.05.24

1ST FLOOR UPPER PLAN

A-01

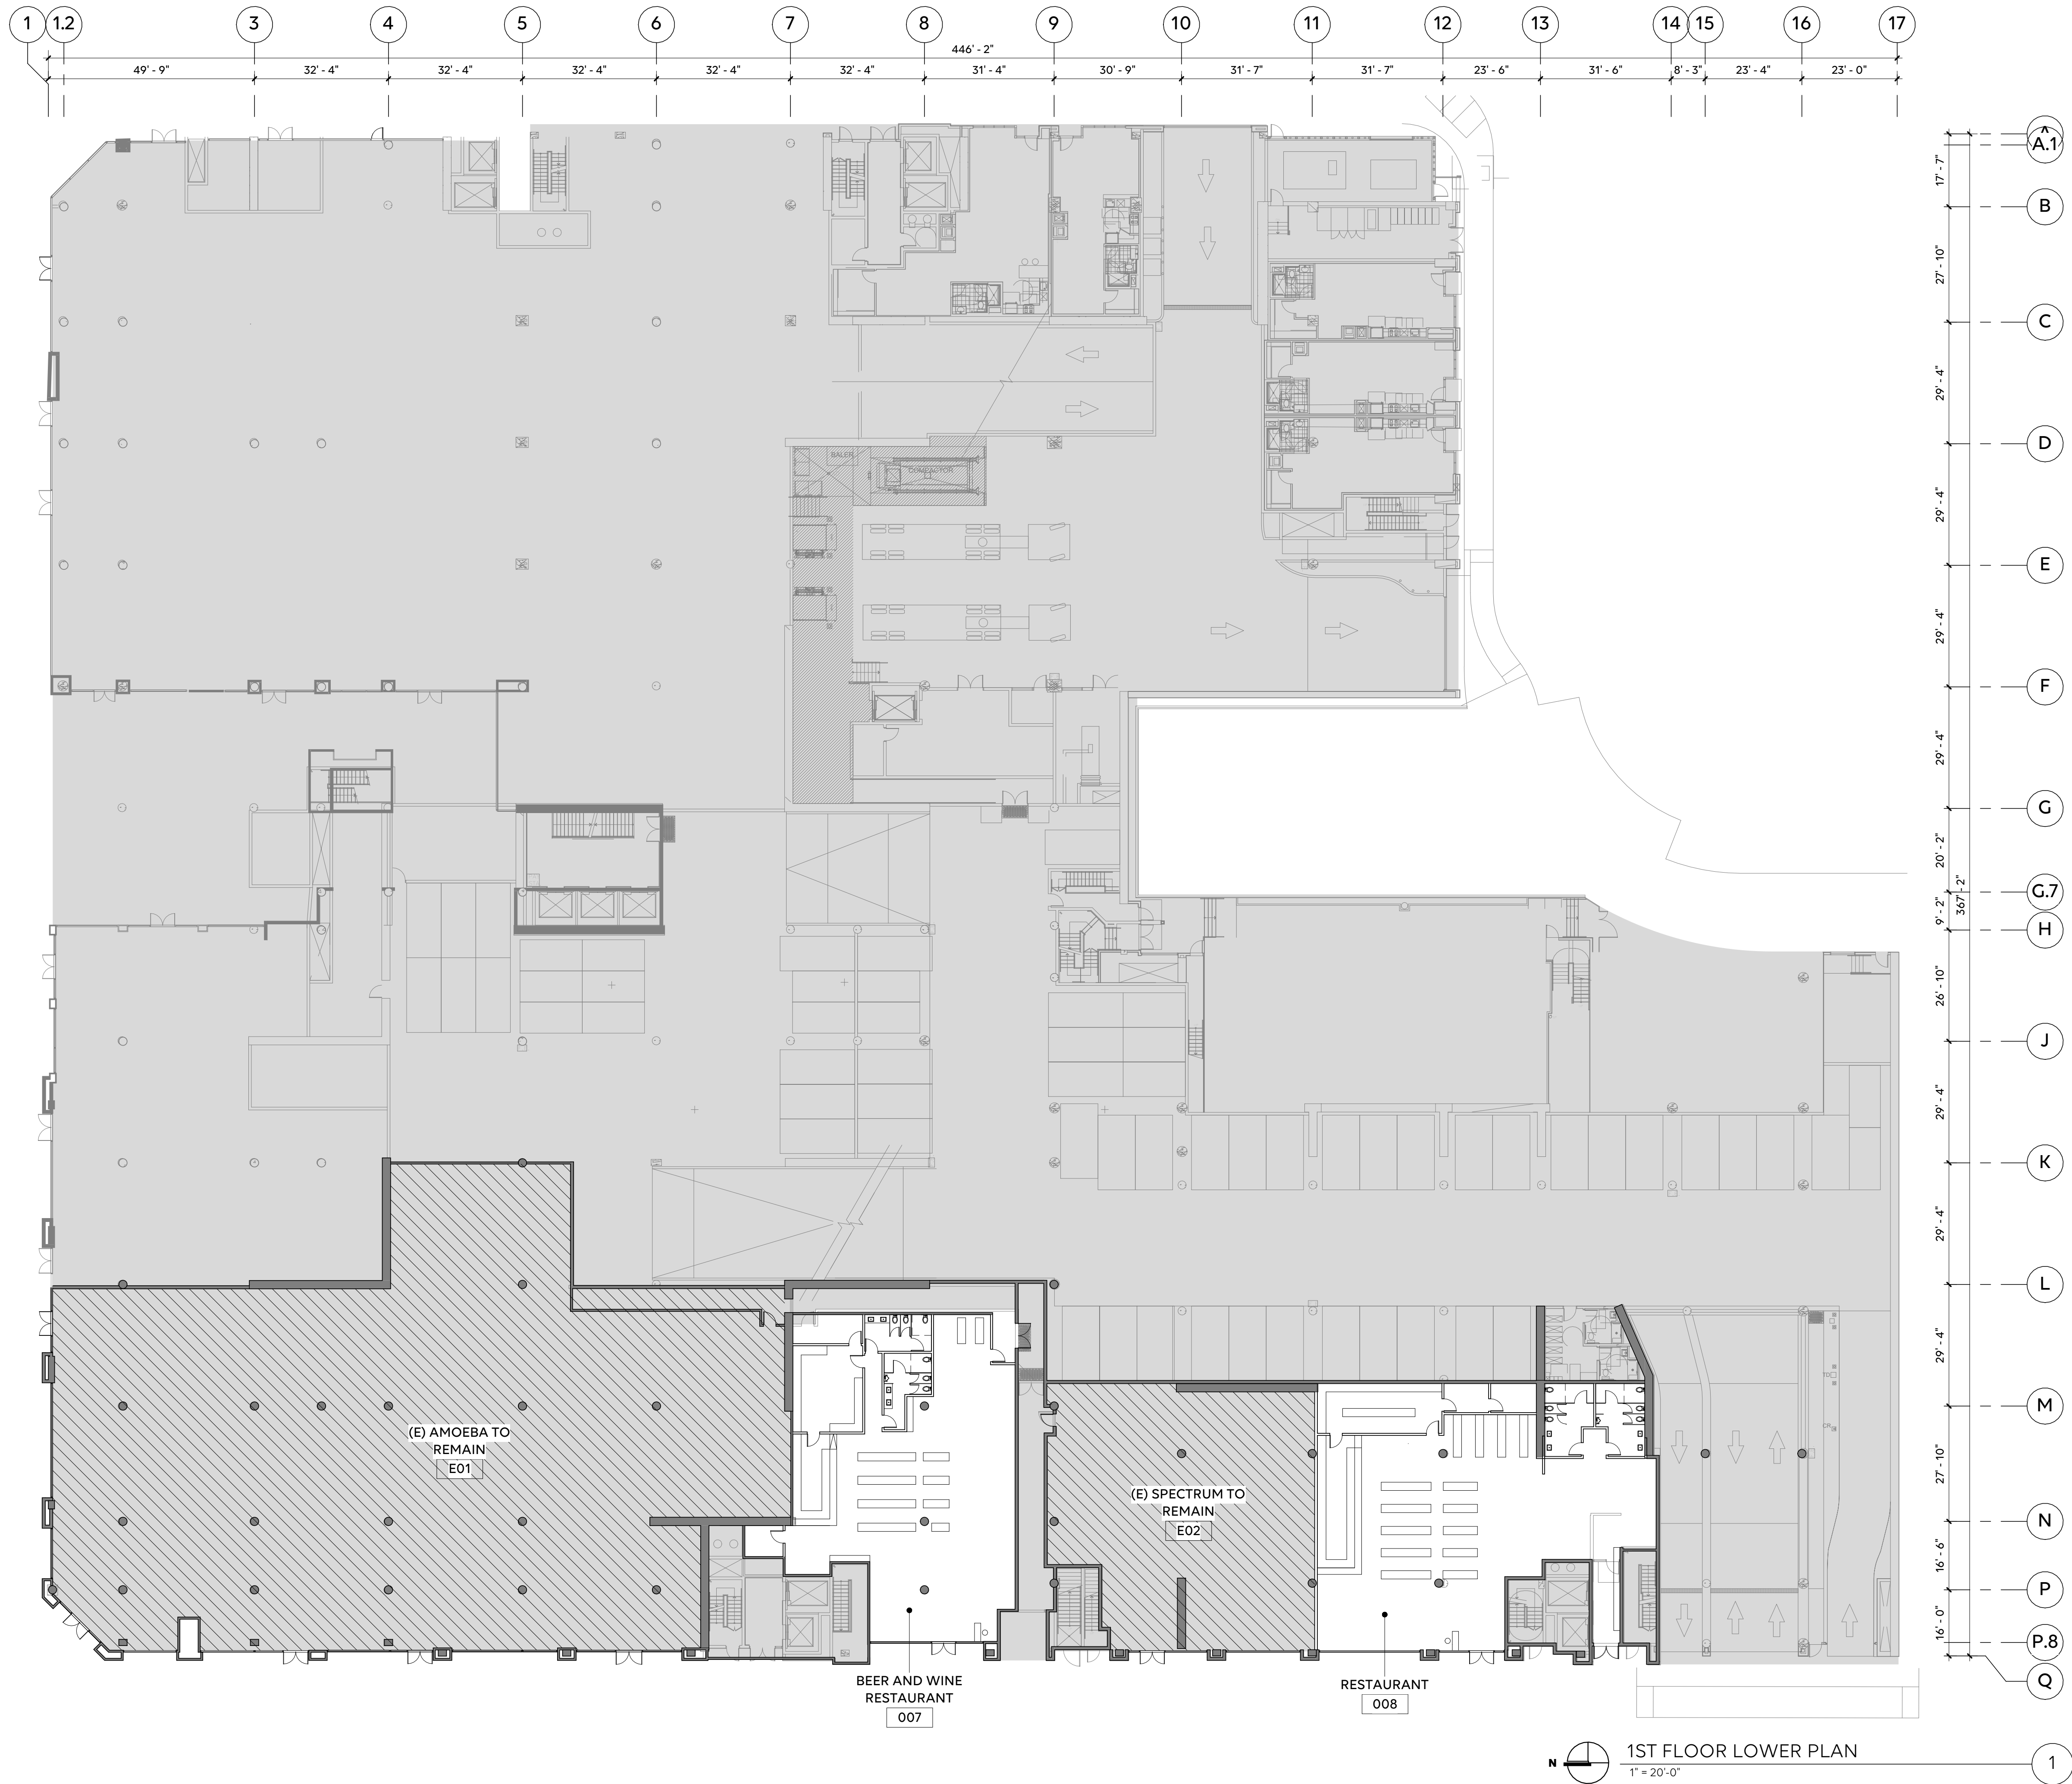

LEGEND

WALL

AREA NOT A PART

(E) TENANT NOT A PART

Plans Approved

as required by

City Los Angeles

Zoning Administrator

ZA-2017-5013-MCUP

Case No.

Ricardo Martinez

Signature

09/17/2024

Date

OMGIWINING

architecture / interiors

1301 N. BROADWAY
LOS ANGELES, CA 90012

EL CENTRO

6200 HOLLYWOOD BLVD.
LOS ANGELES, CA 90028

CUP/CUB PLAN

REVISIONS:

08.05.24

1ST FLOOR LOWER
PLAN


A-02

Plans Approved

as required by
City Los Angeles
Zoning Administrator
ZA-2017-5013-MCUP

Case No.
Ricardo Martinez
Signature
09/17/2024
Date

RESTAURANT - 003		
Name	Area	SEAT COUNT
ALCOHOL STORAGE	66 SF	
BAR	138 SF	13
DINING	1304 SF	124
KITCHEN	187 SF	
RESTROOM - MEN	106 SF	
RESTROOM - WOMEN	101 SF	
WALK IN FRIDGE	46 SF	
Grand total	1947 SF	137

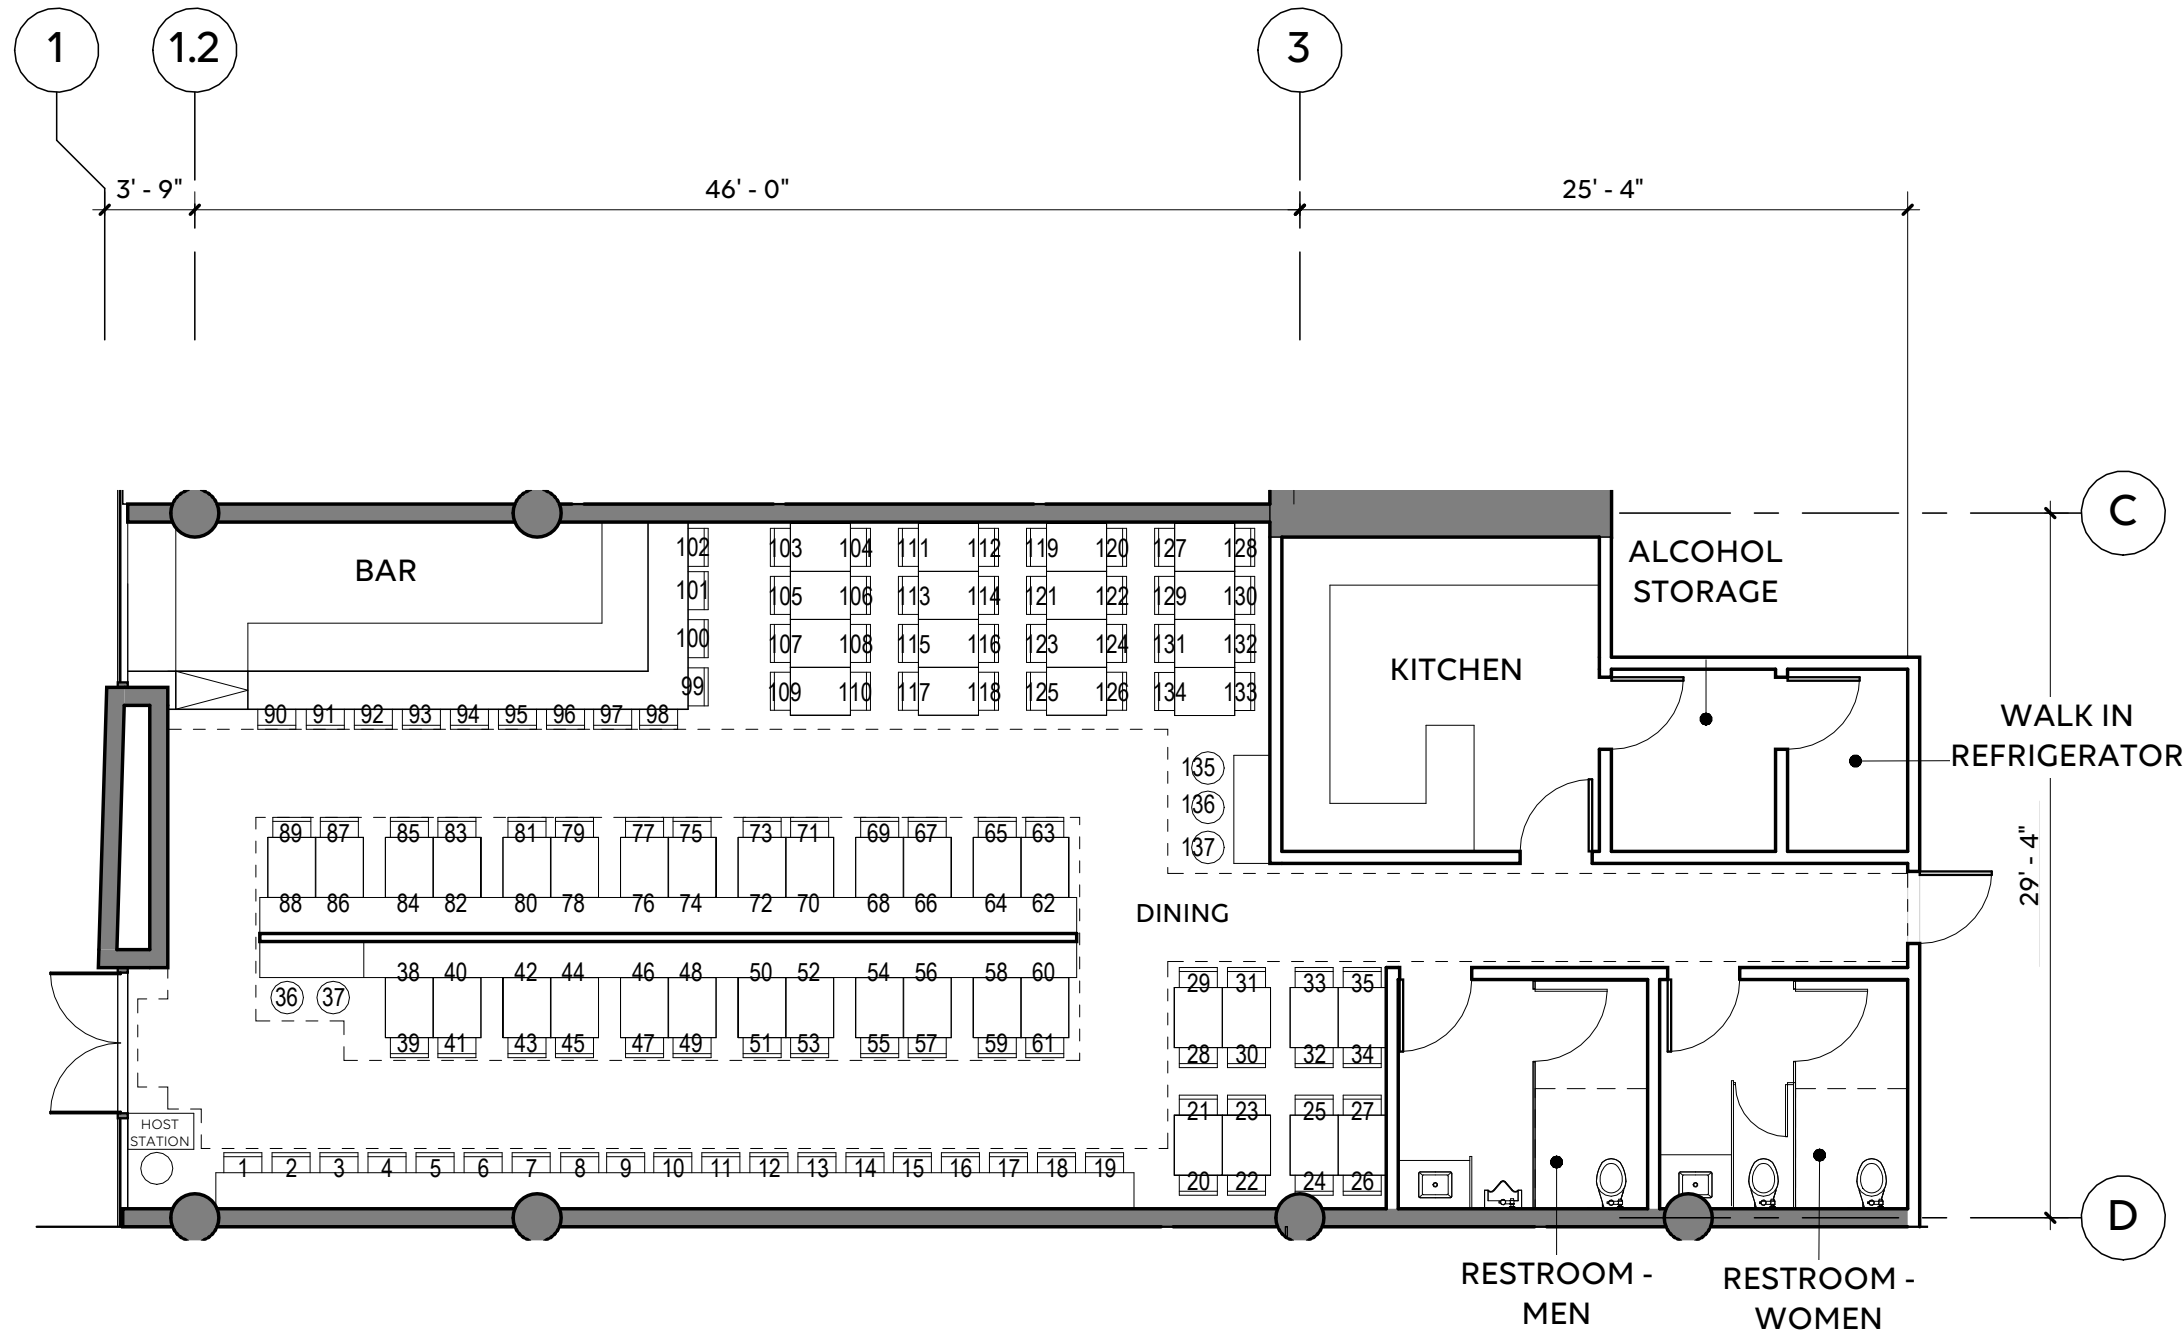


RESTAURANT - 003

1/8" = 1'-0"

9

BEER AND WINE RESTAURANT - 002		
Name	Area	SEAT COUNT
ALCOHOL STORAGE	69 SF	
BAR	220 SF	14
DINING	1263 SF	106
KITCHEN	182 SF	
RESTROOM - MEN	103 SF	
RESTROOM - WOMEN	106 SF	
STORAGE	24 SF	
WALK IN FRIDGE	62 SF	
Grand total	2029 SF	120

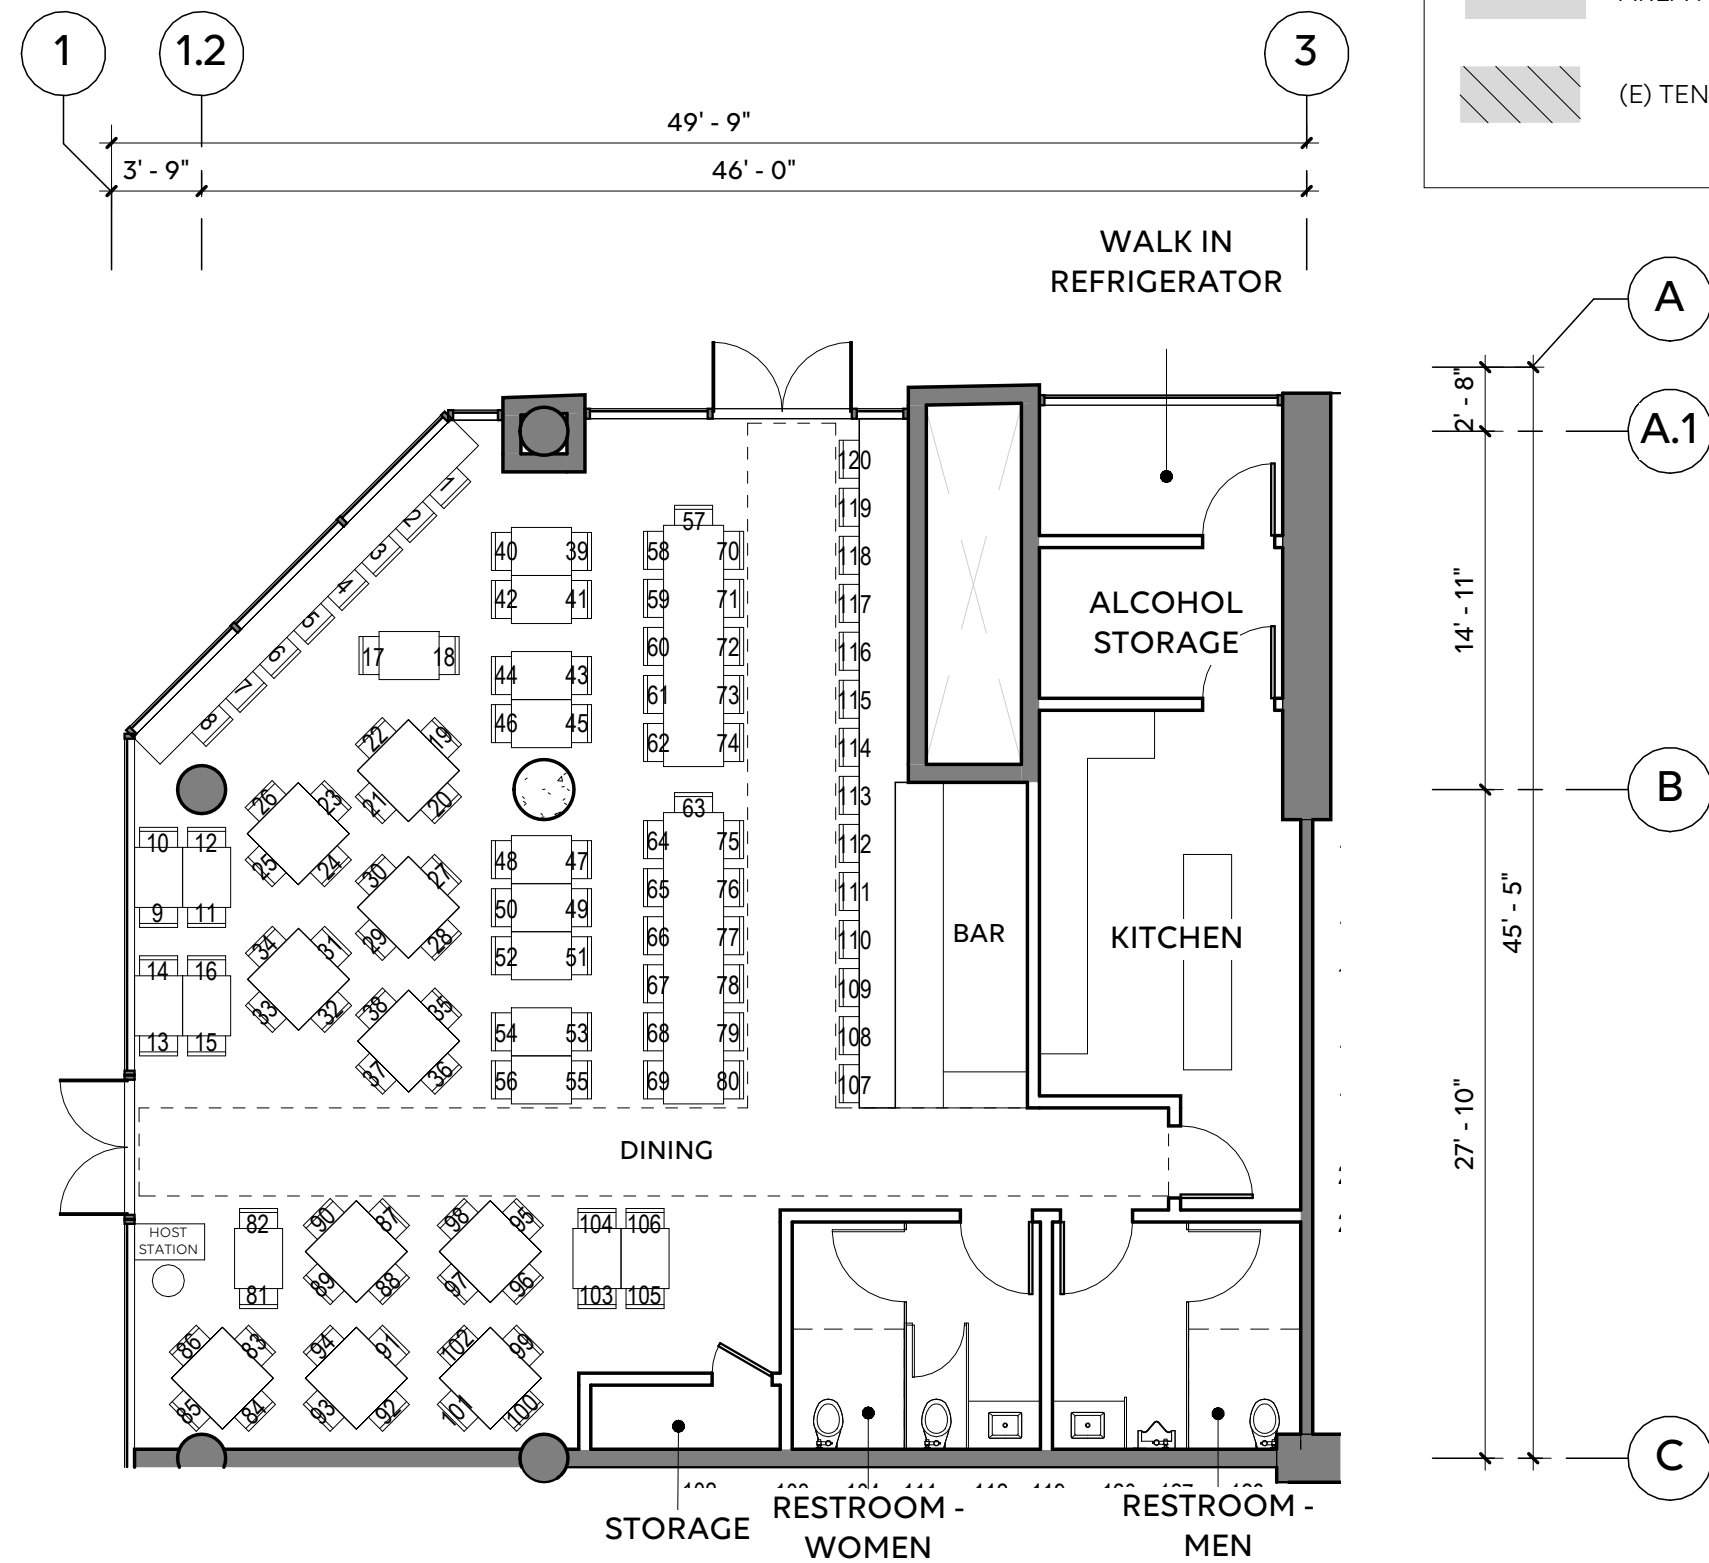


BEER AND WINE RESTAURANT - 002

1/8" = 1'-0"

3

RESTAURANT - 001		
Name	Area	SEAT COUNT
ALCOHOL STORAGE	62 SF	
BAR	200 SF	8
DINING	1254 SF	118
KITCHEN	240 SF	
RESTROOM - MEN	122 SF	
RESTROOM - WOMEN	127 SF	
WALK IN FRIDGE	65 SF	
Grand total	2069 SF	126

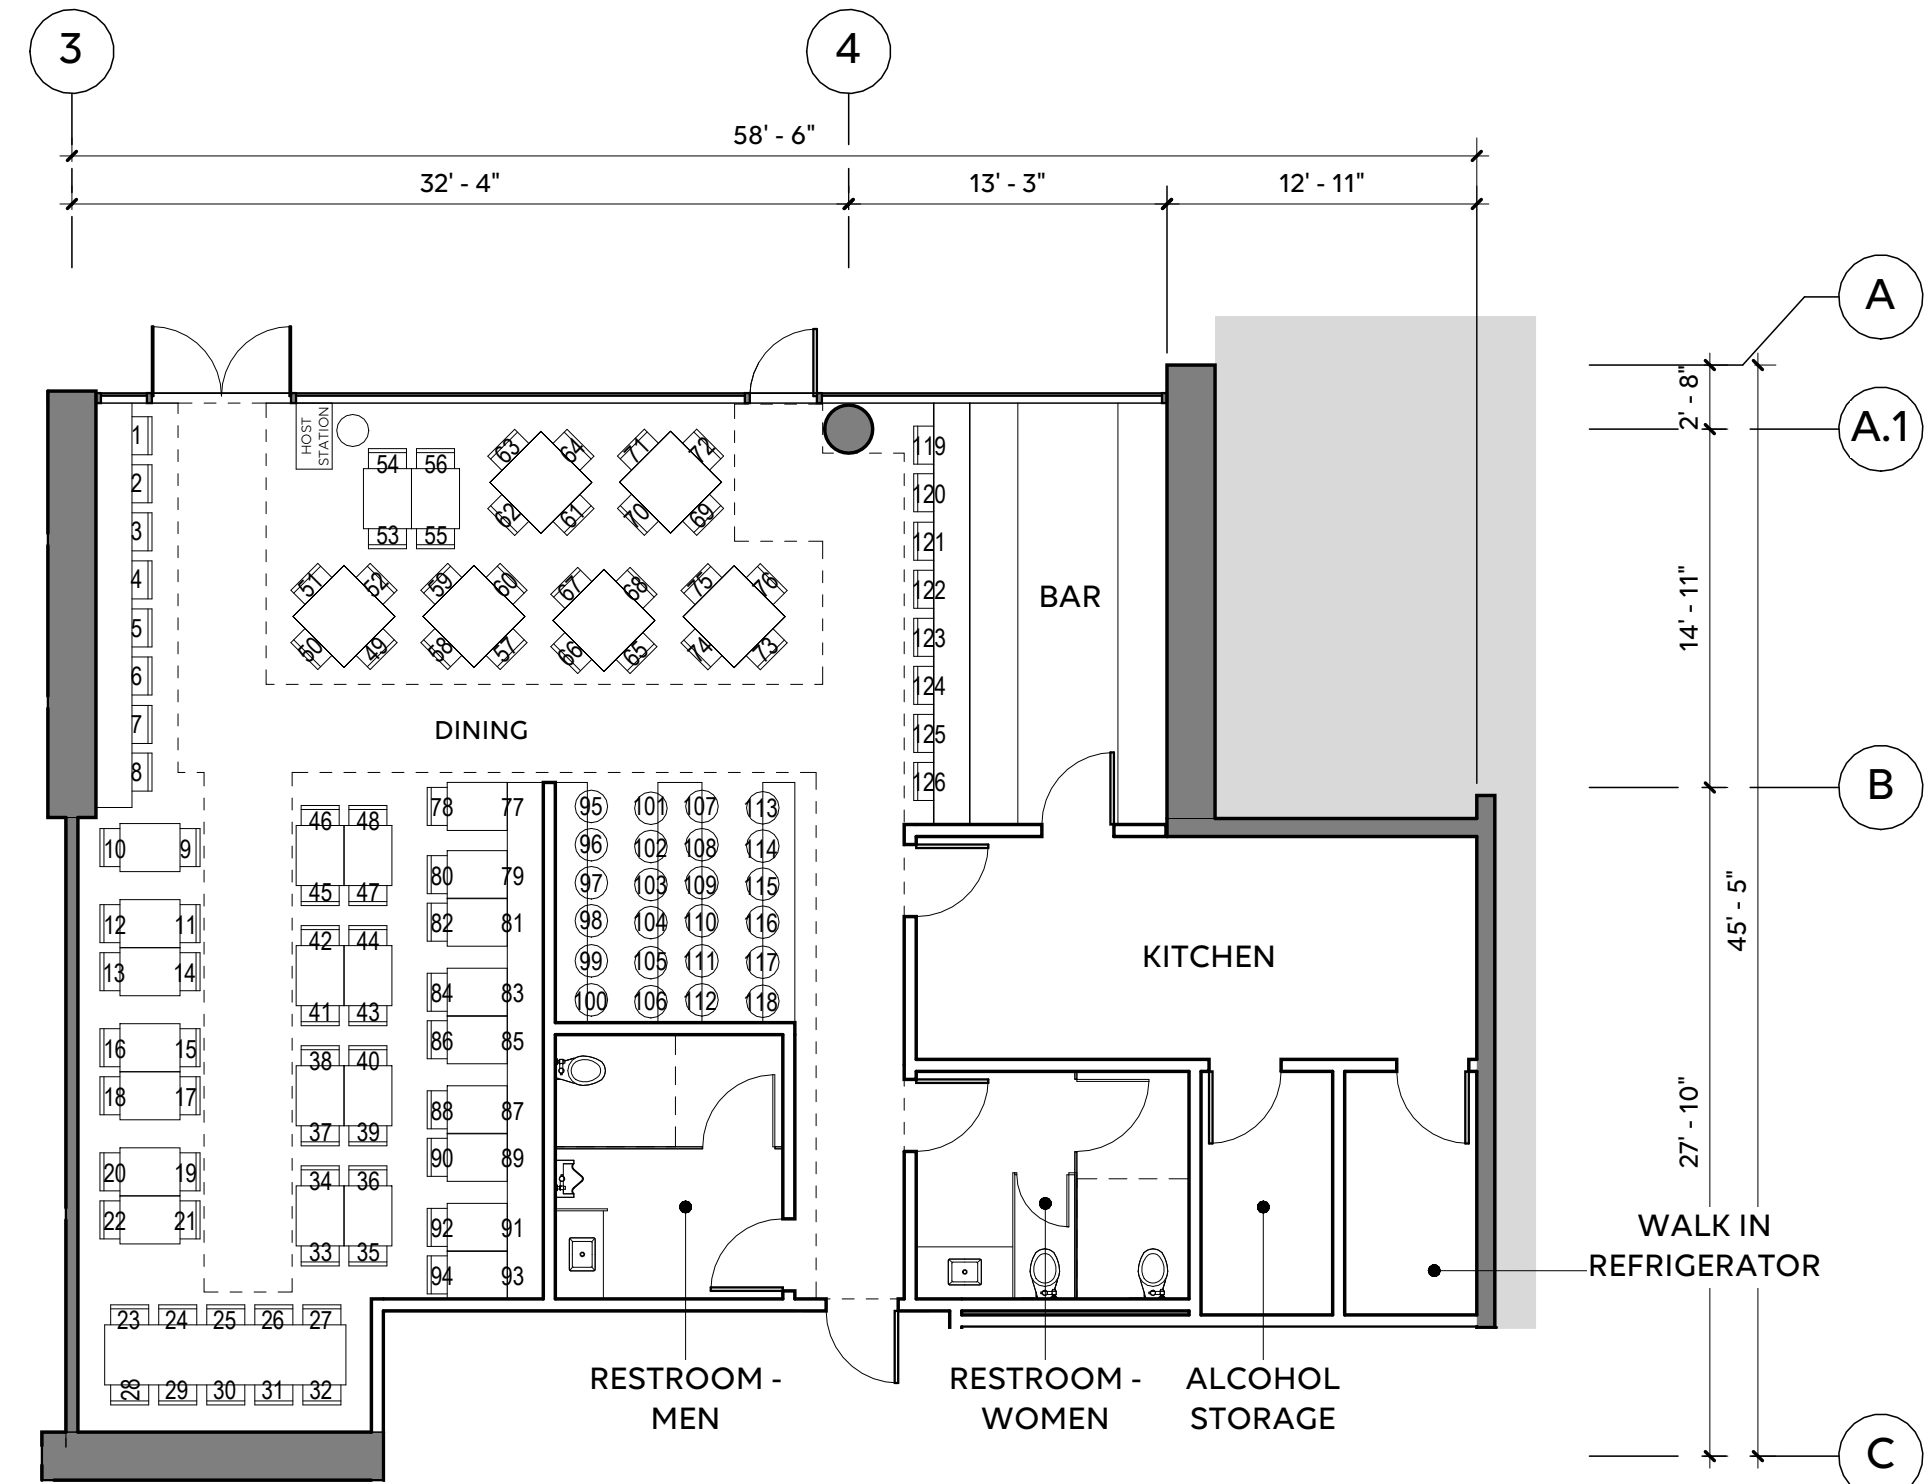

RESTAURANT - 001

1/8" = 1'-0"

1

LEGEND

- WALL
- AREA NOT A PART
- (E) TENANT NOT A PART

OMGI VNNING
architecture / interiors

1301 N. BROADWAY
LOS ANGELES, CA 90012

EL CENTRO
6200 HOLLYWOOD BLVD.
LOS ANGELES, CA 90028

CUP/CUB PLAN

REVISIONS:

08.05.24

CUP/CUB PLAN

A-10

8/5/2024 8:05:13 PM

THIS DRAWING AND THE INFORMATION CONTAINED HEREIN ARE THE COPYRIGHTED WORK OF OMGIVNING ARCHITECTS AND MAY NOT BE REPRODUCED WITHOUT WRITTEN PERMISSION.

Plans Approved


as required by
City Los Angeles
Zoning Administrator

ZA-2017-5013-MCUP


Case No.
Ricardo Martinez

Signature
09/17/2024

Date

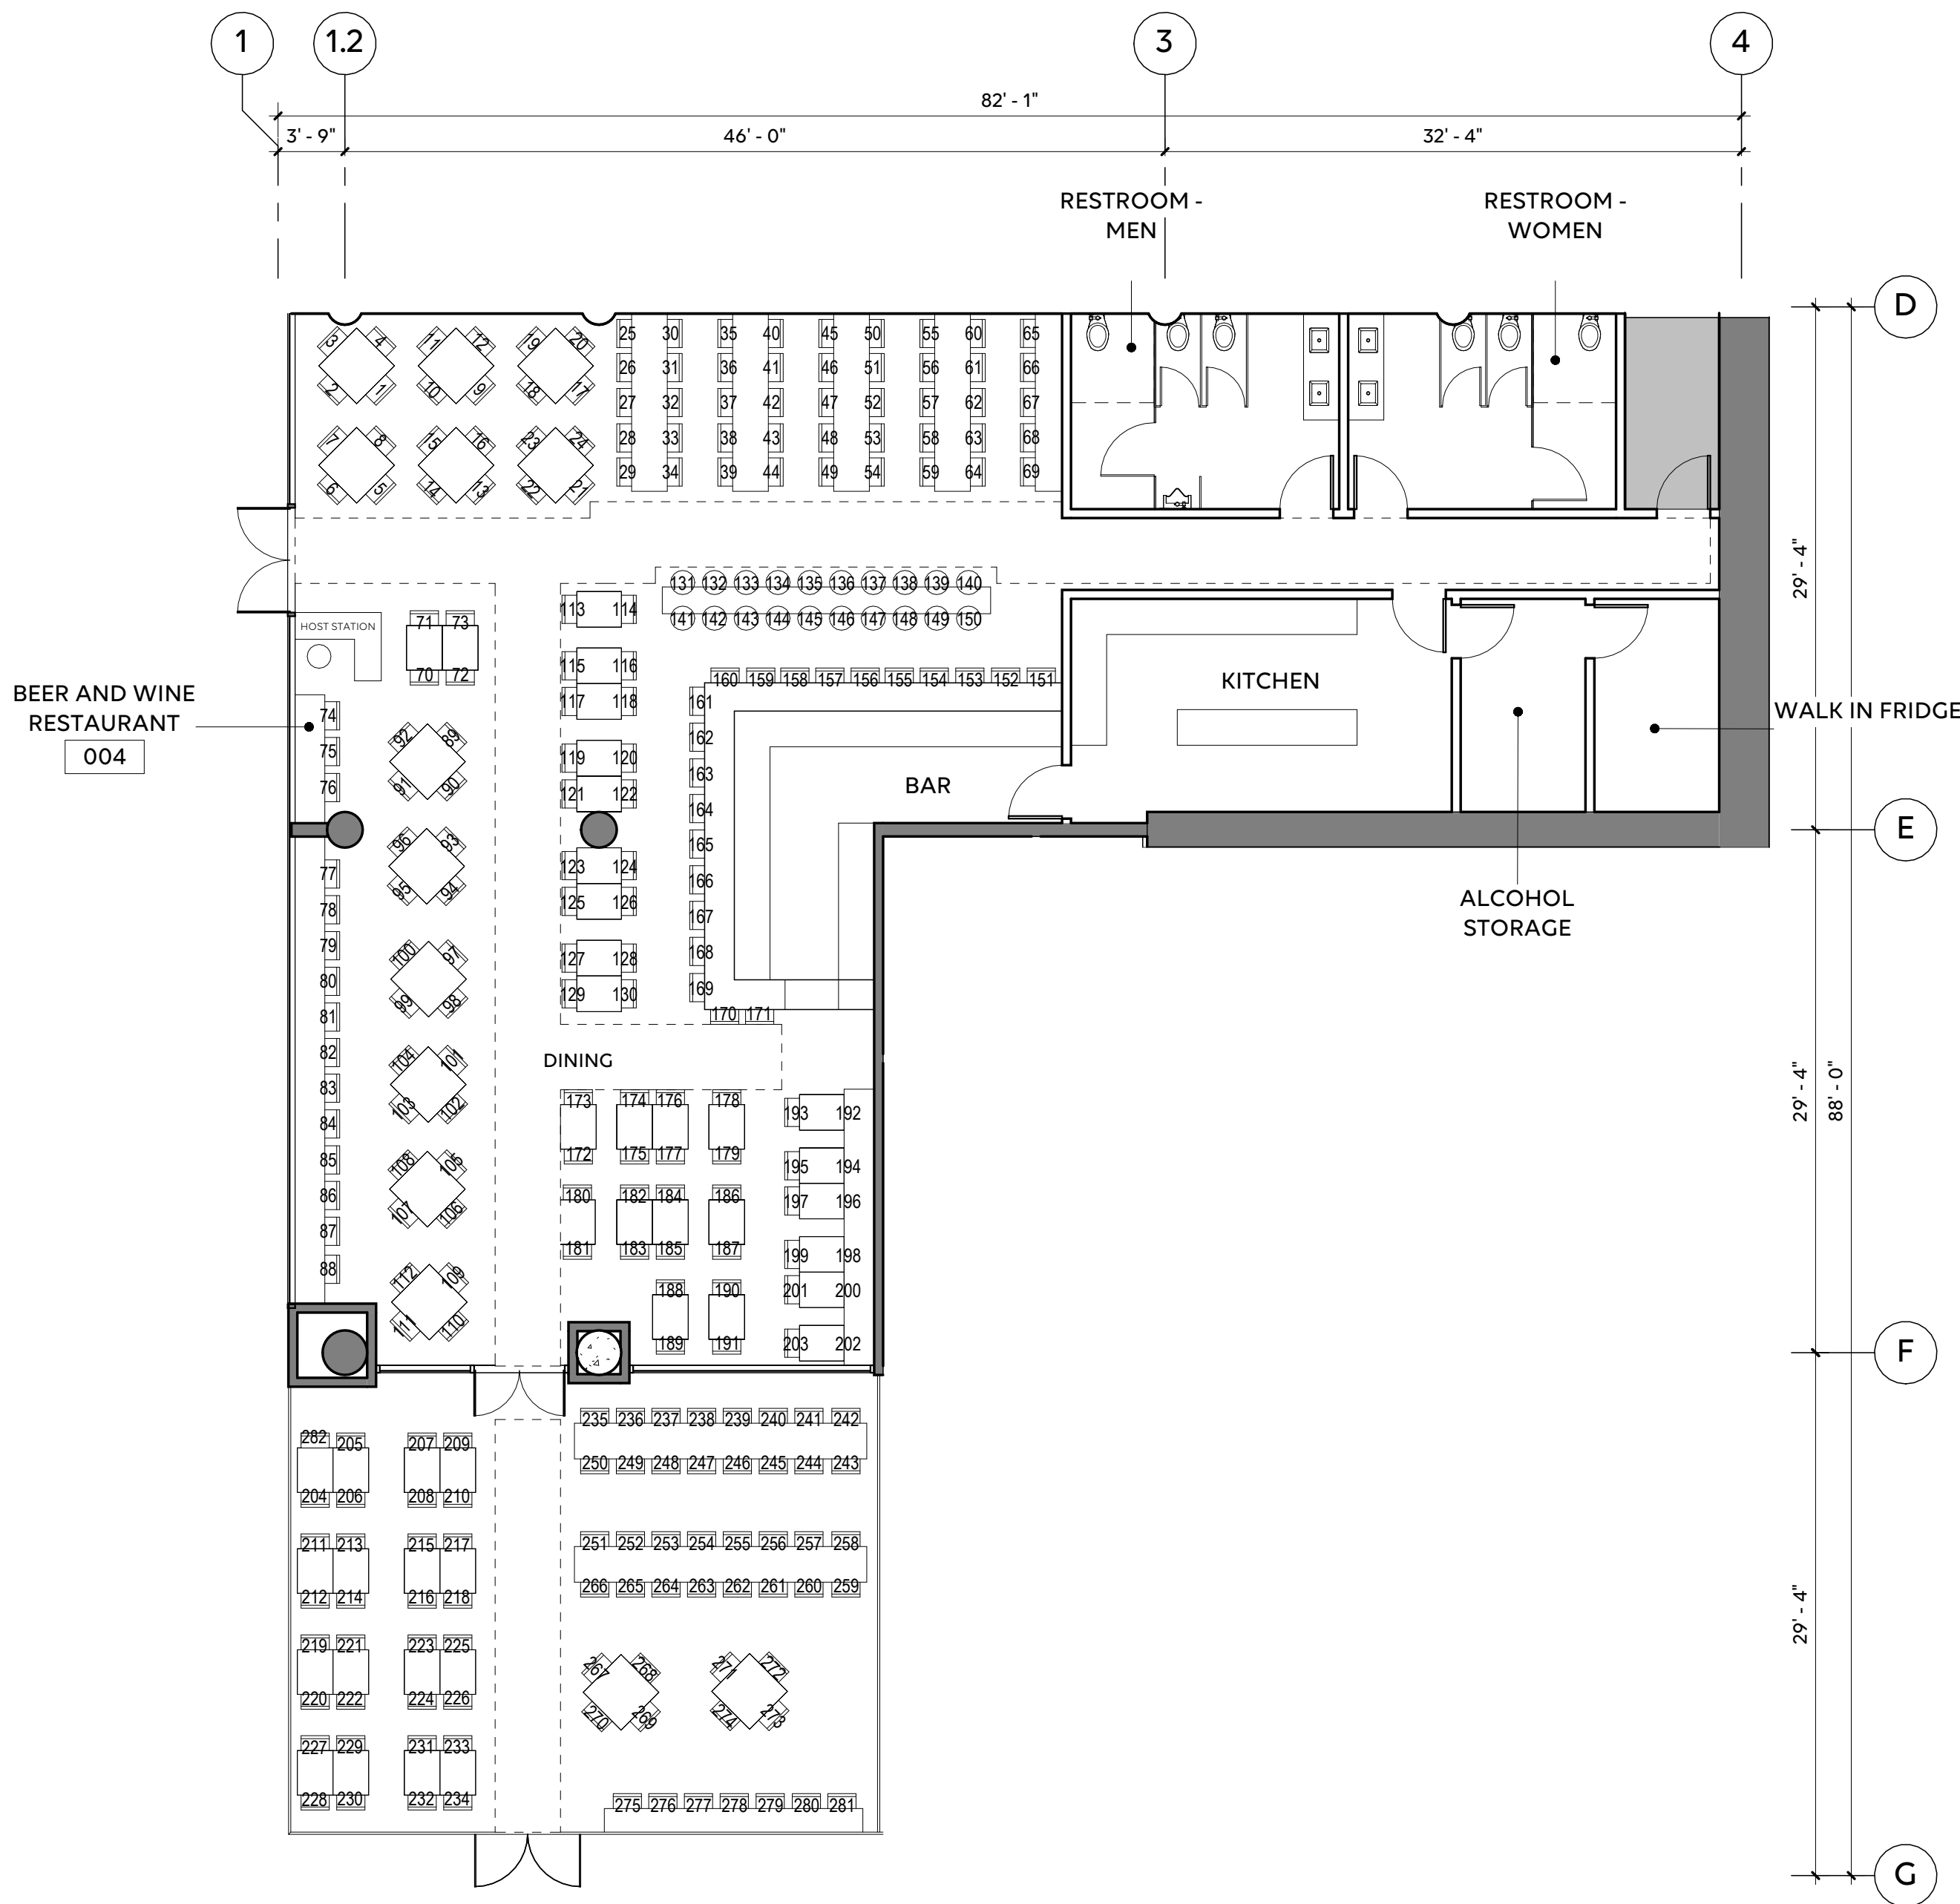

BEER AND WINE RESTAURANT - 004		
NAME	AREA	SEAT COUNT
ALCOHOL STORAGE	95 SF	
BAR	259 SF	21
INDOOR DINING	2154 SF	182
KITCHEN	270 SF	
OUTDOOR DINING	863 SF	79
RESTROOM - MEN	174 SF	
RESTROOM - WOMEN	174 SF	
WALK IN FRIDGE	84 SF	
Grand total	4074 SF	282

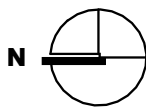

BEER AND WINE RESTAURANT - 004
1/8" = 1'-0"

1

LEGEND

- WALL
- AREA NOT A PART
- (E) TENANT NOT A PART

OMGIVNING
architecture / interiors

1301 N. BROADWAY
LOS ANGELES, CA 90012

EL CENTRO
6200 HOLLYWOOD BLVD.
LOS ANGELES, CA 90028
CUP/CUB PLAN

REVISIONS:

08.05.24

CUP/CUB PLAN

A-11


8/5/2024 8:05:15 PM

THIS DRAWING AND THE INFORMATION CONTAINED HEREIN ARE THE COPYRIGHTED WORK OF OMGIVNING ARCHITECTS AND MAY NOT BE REPRODUCED WITHOUT WRITTEN PERMISSION.

Plans Approved

as required by
City Los Angeles
Zoning Administrator
ZA-2017-5013-MCUP
Case No.
Ricardo Martinez
Signature
09/17/2024
Date

RESTAURANT - 005		
Name	Area	SEAT COUNT
ALCOHOL STORAGE	108 SF	
BAR	425 SF	17
INDOOR DINING	2196 SF	229
KITCHEN	311 SF	
OUTDOOR DINING	920 SF	76
RESTROOM - WOMEN	205 SF	
RESTROOM - MEN	175 SF	
STORAGE	20 SF	
WALK IN FRIDGE	123 SF	
Grand total	4483 SF	322

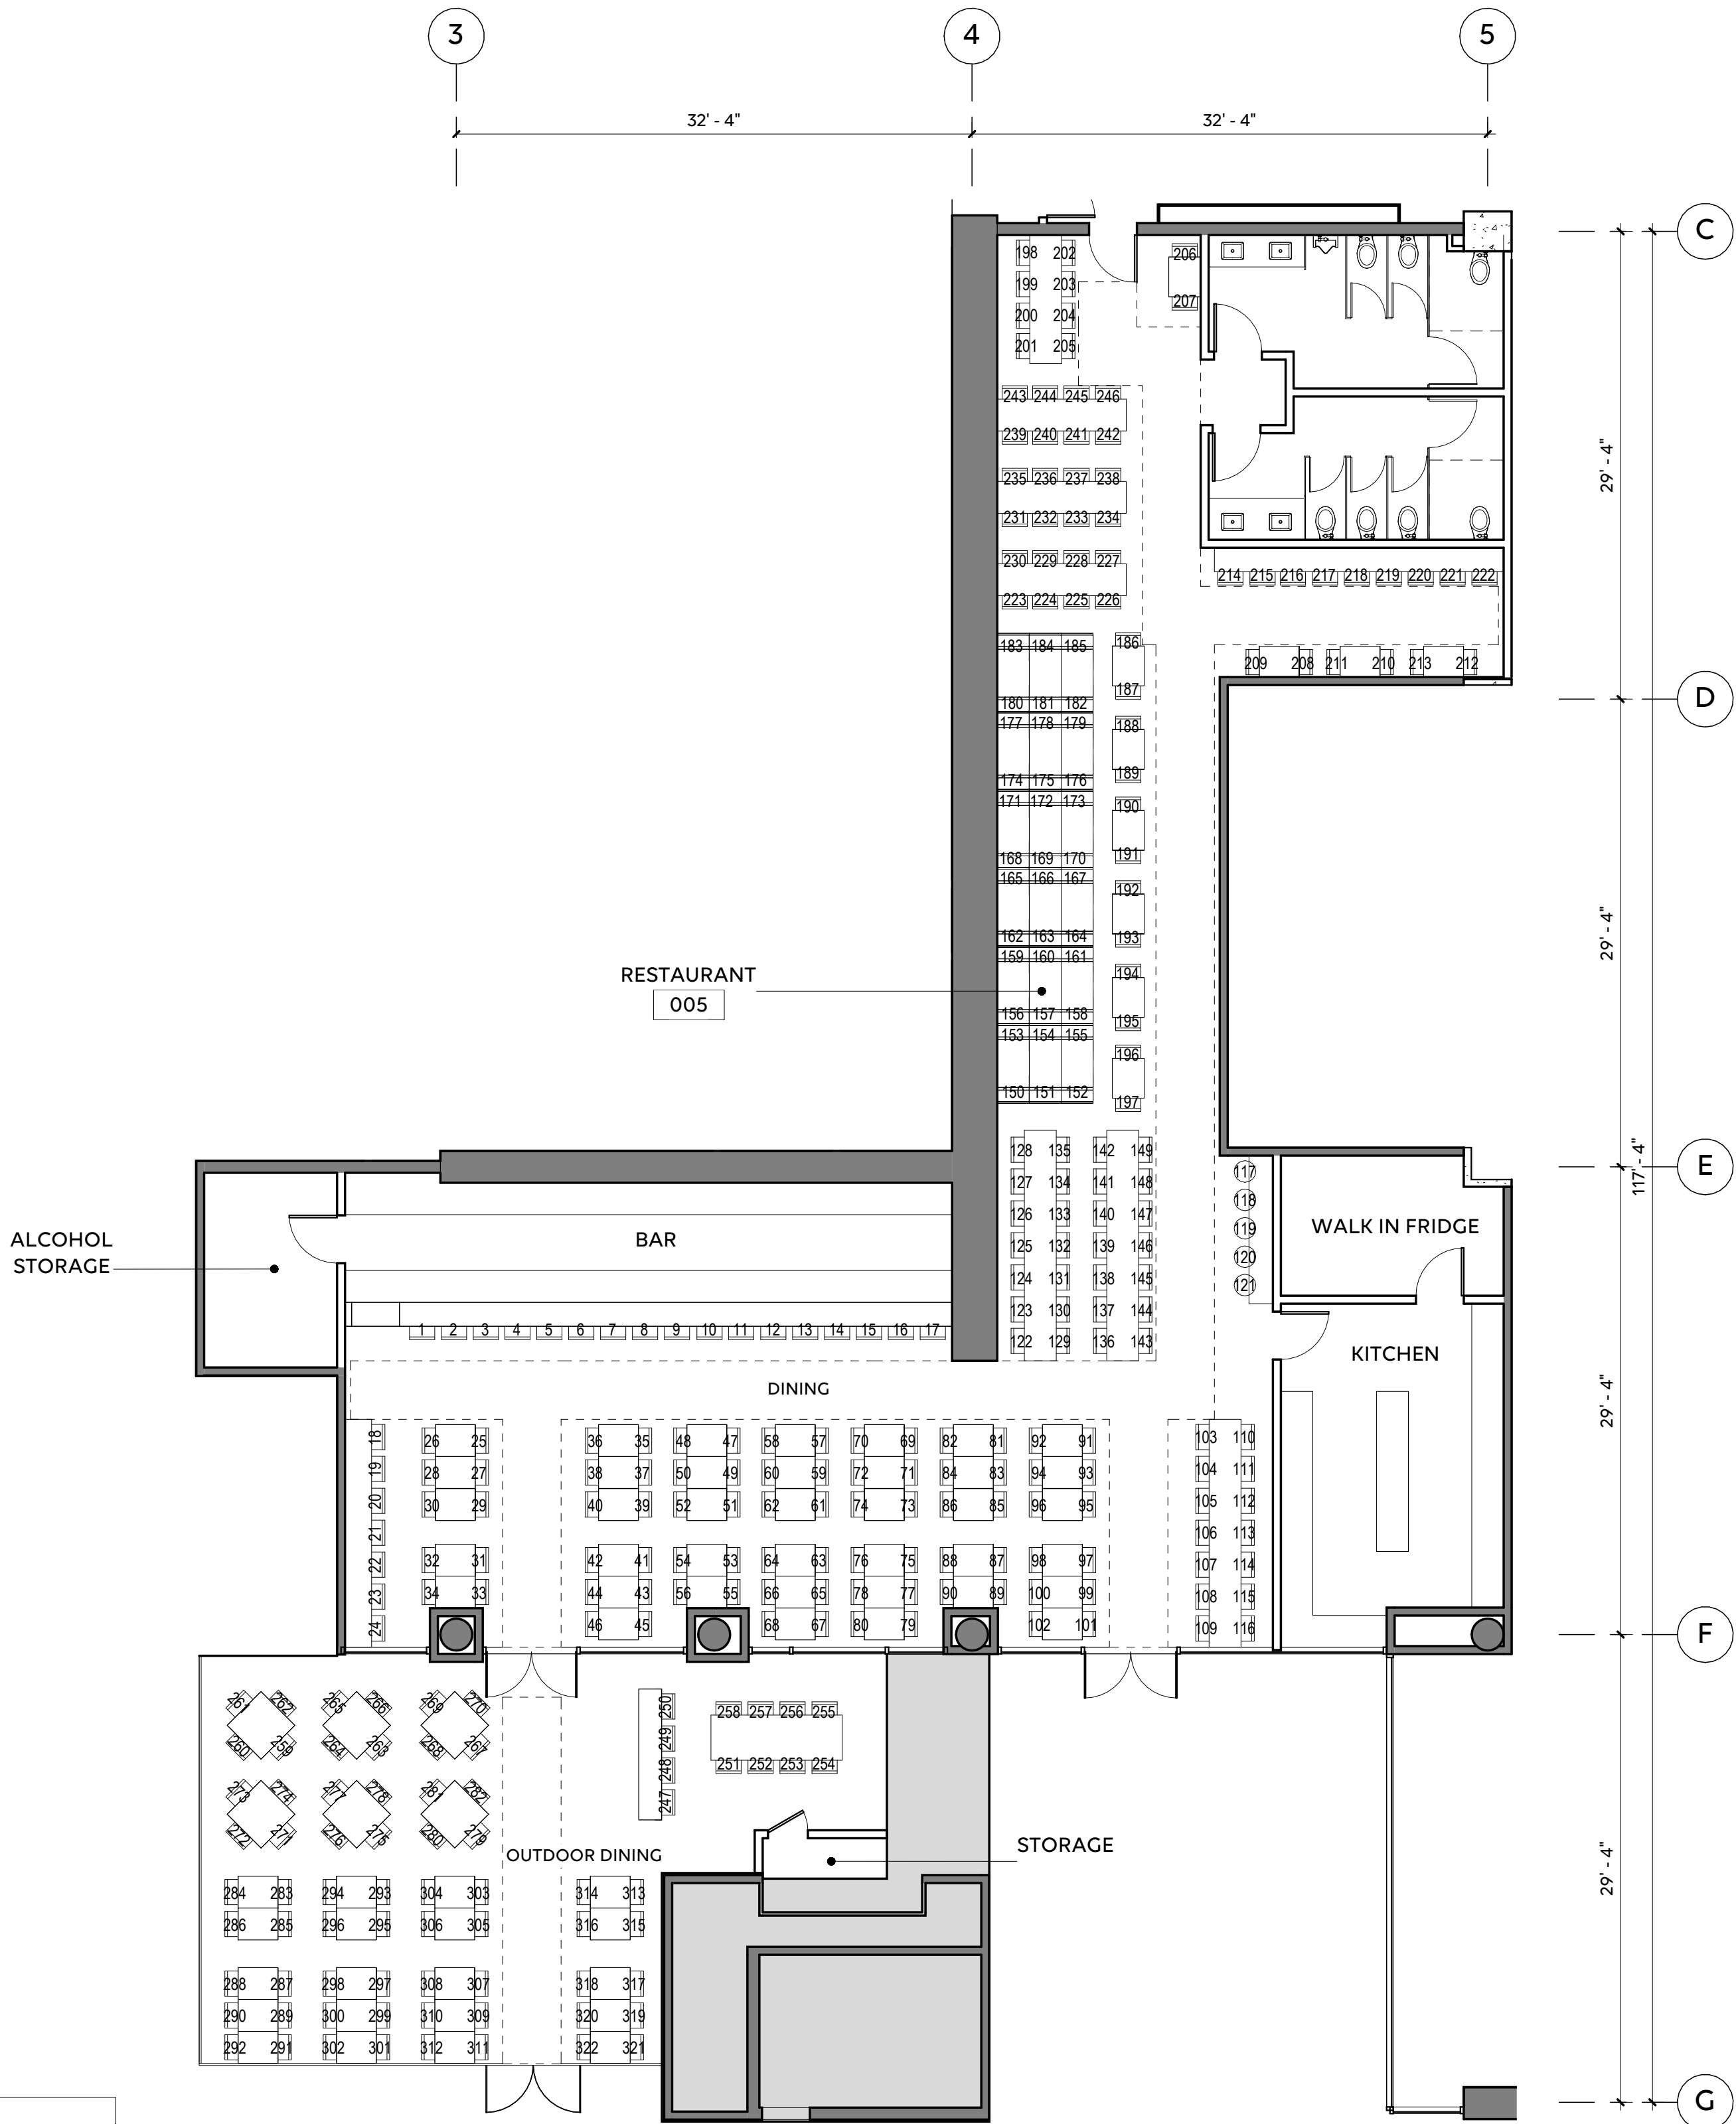

LEGEND

WALL

AREA NOT A PART

OMGIVNING
architecture / interiors

1301 N. BROADWAY
LOS ANGELES, CA 90012

EL CENTRO
6200 HOLLYWOOD BLVD.
LOS ANGELES, CA 90028

CUP/CUB PLAN

REVISIONS:

08.05.24

CUP/CUB PLAN

A-12

Plans Approved

as required by

City Los Angeles

Zoning Administrator

ZA-2017-5013-MCUP


Case No.

Ricardo Martinez

Signature

09/17/2024


Date

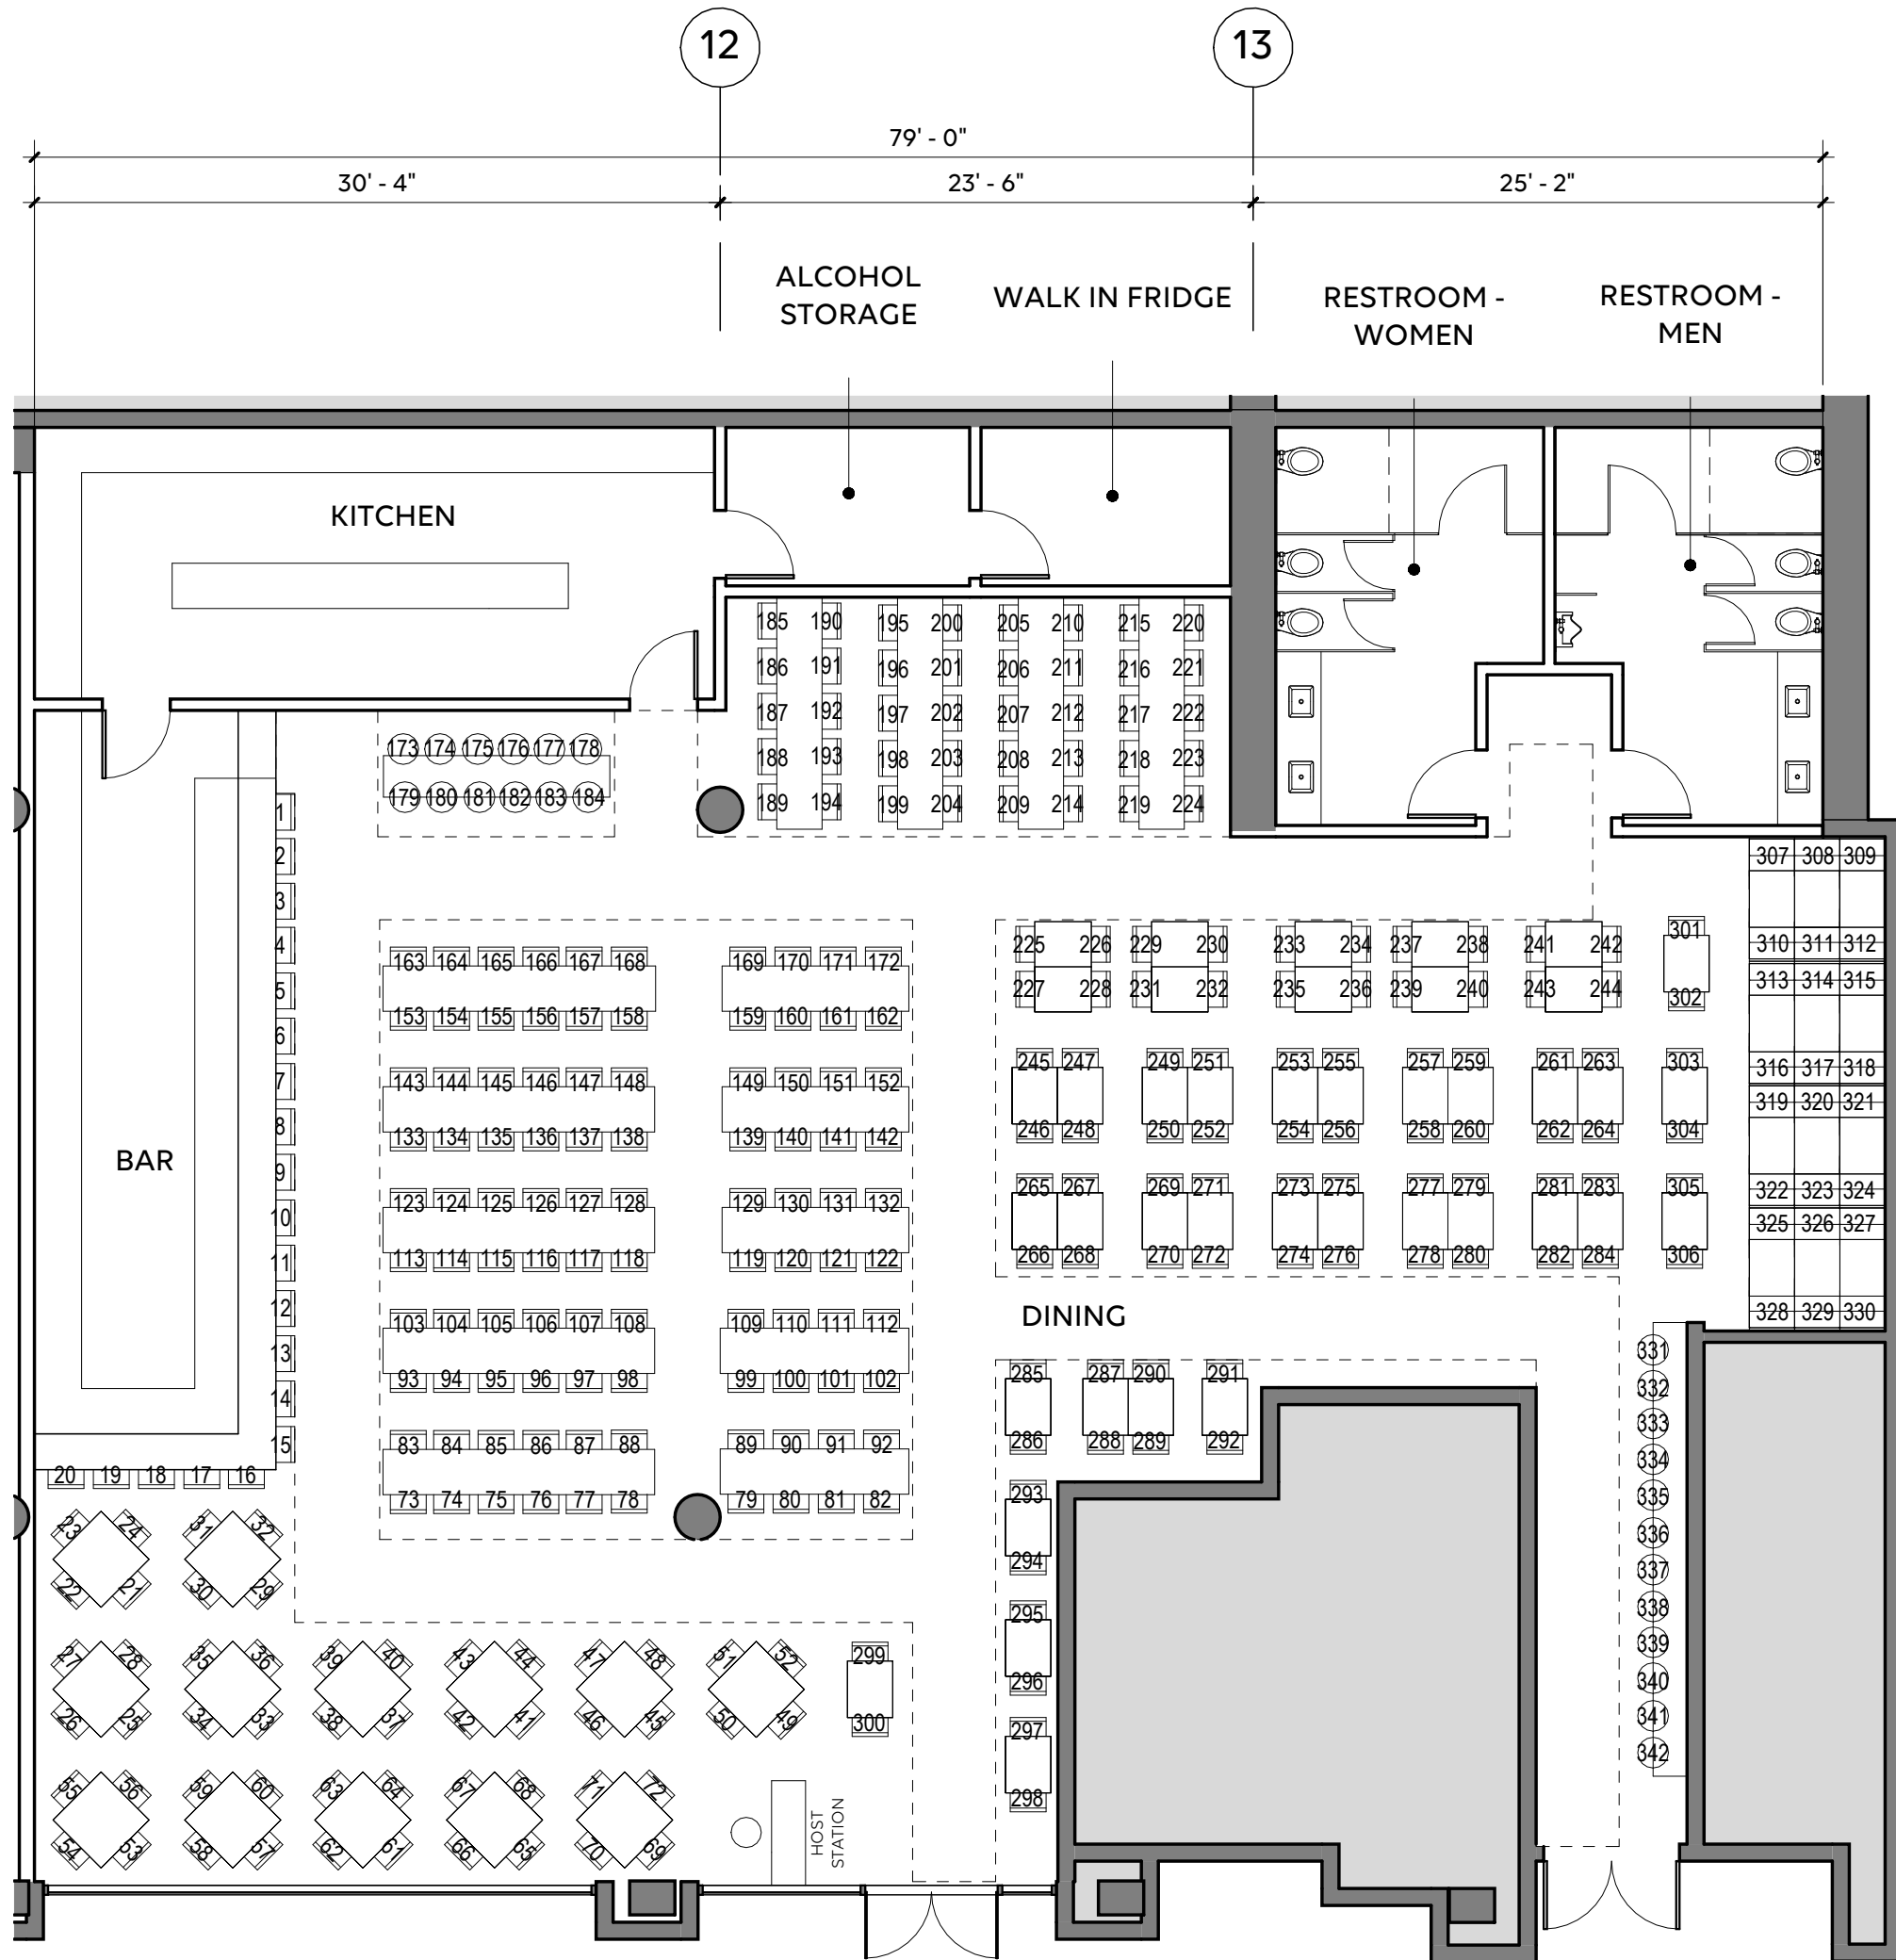


RESTAURANT - 008
1/8" = 1'-0"

BEER AND WINE RESTAURANT - 007		
Name	Area	SEAT COUNT
ALCOHOL STORAGE	103 SF	0
BAR	198 SF	13
DINING	2790 SF	262
KITCHEN	369 SF	0
RESTROOM - MEN	170 SF	0
RESTROOM - WOMEN	142 SF	0
WALK IN FRIDGE	133 SF	0
Grand total	3904 SF	275

BEER AND WINE RESTAURANT - 006		
Name	Area	SEAT COUNT
ALCOHOL STORAGE	114 SF	
BAR/KITCHEN	375 SF	
INDOOR DINING	694 SF	48
OUTDOOR DINING	508 SF	51
RESTROOM - MEN	51 SF	
RESTROOM - WOMEN	105 SF	
STORAGE	50 SF	
Grand total	1896 SF	99

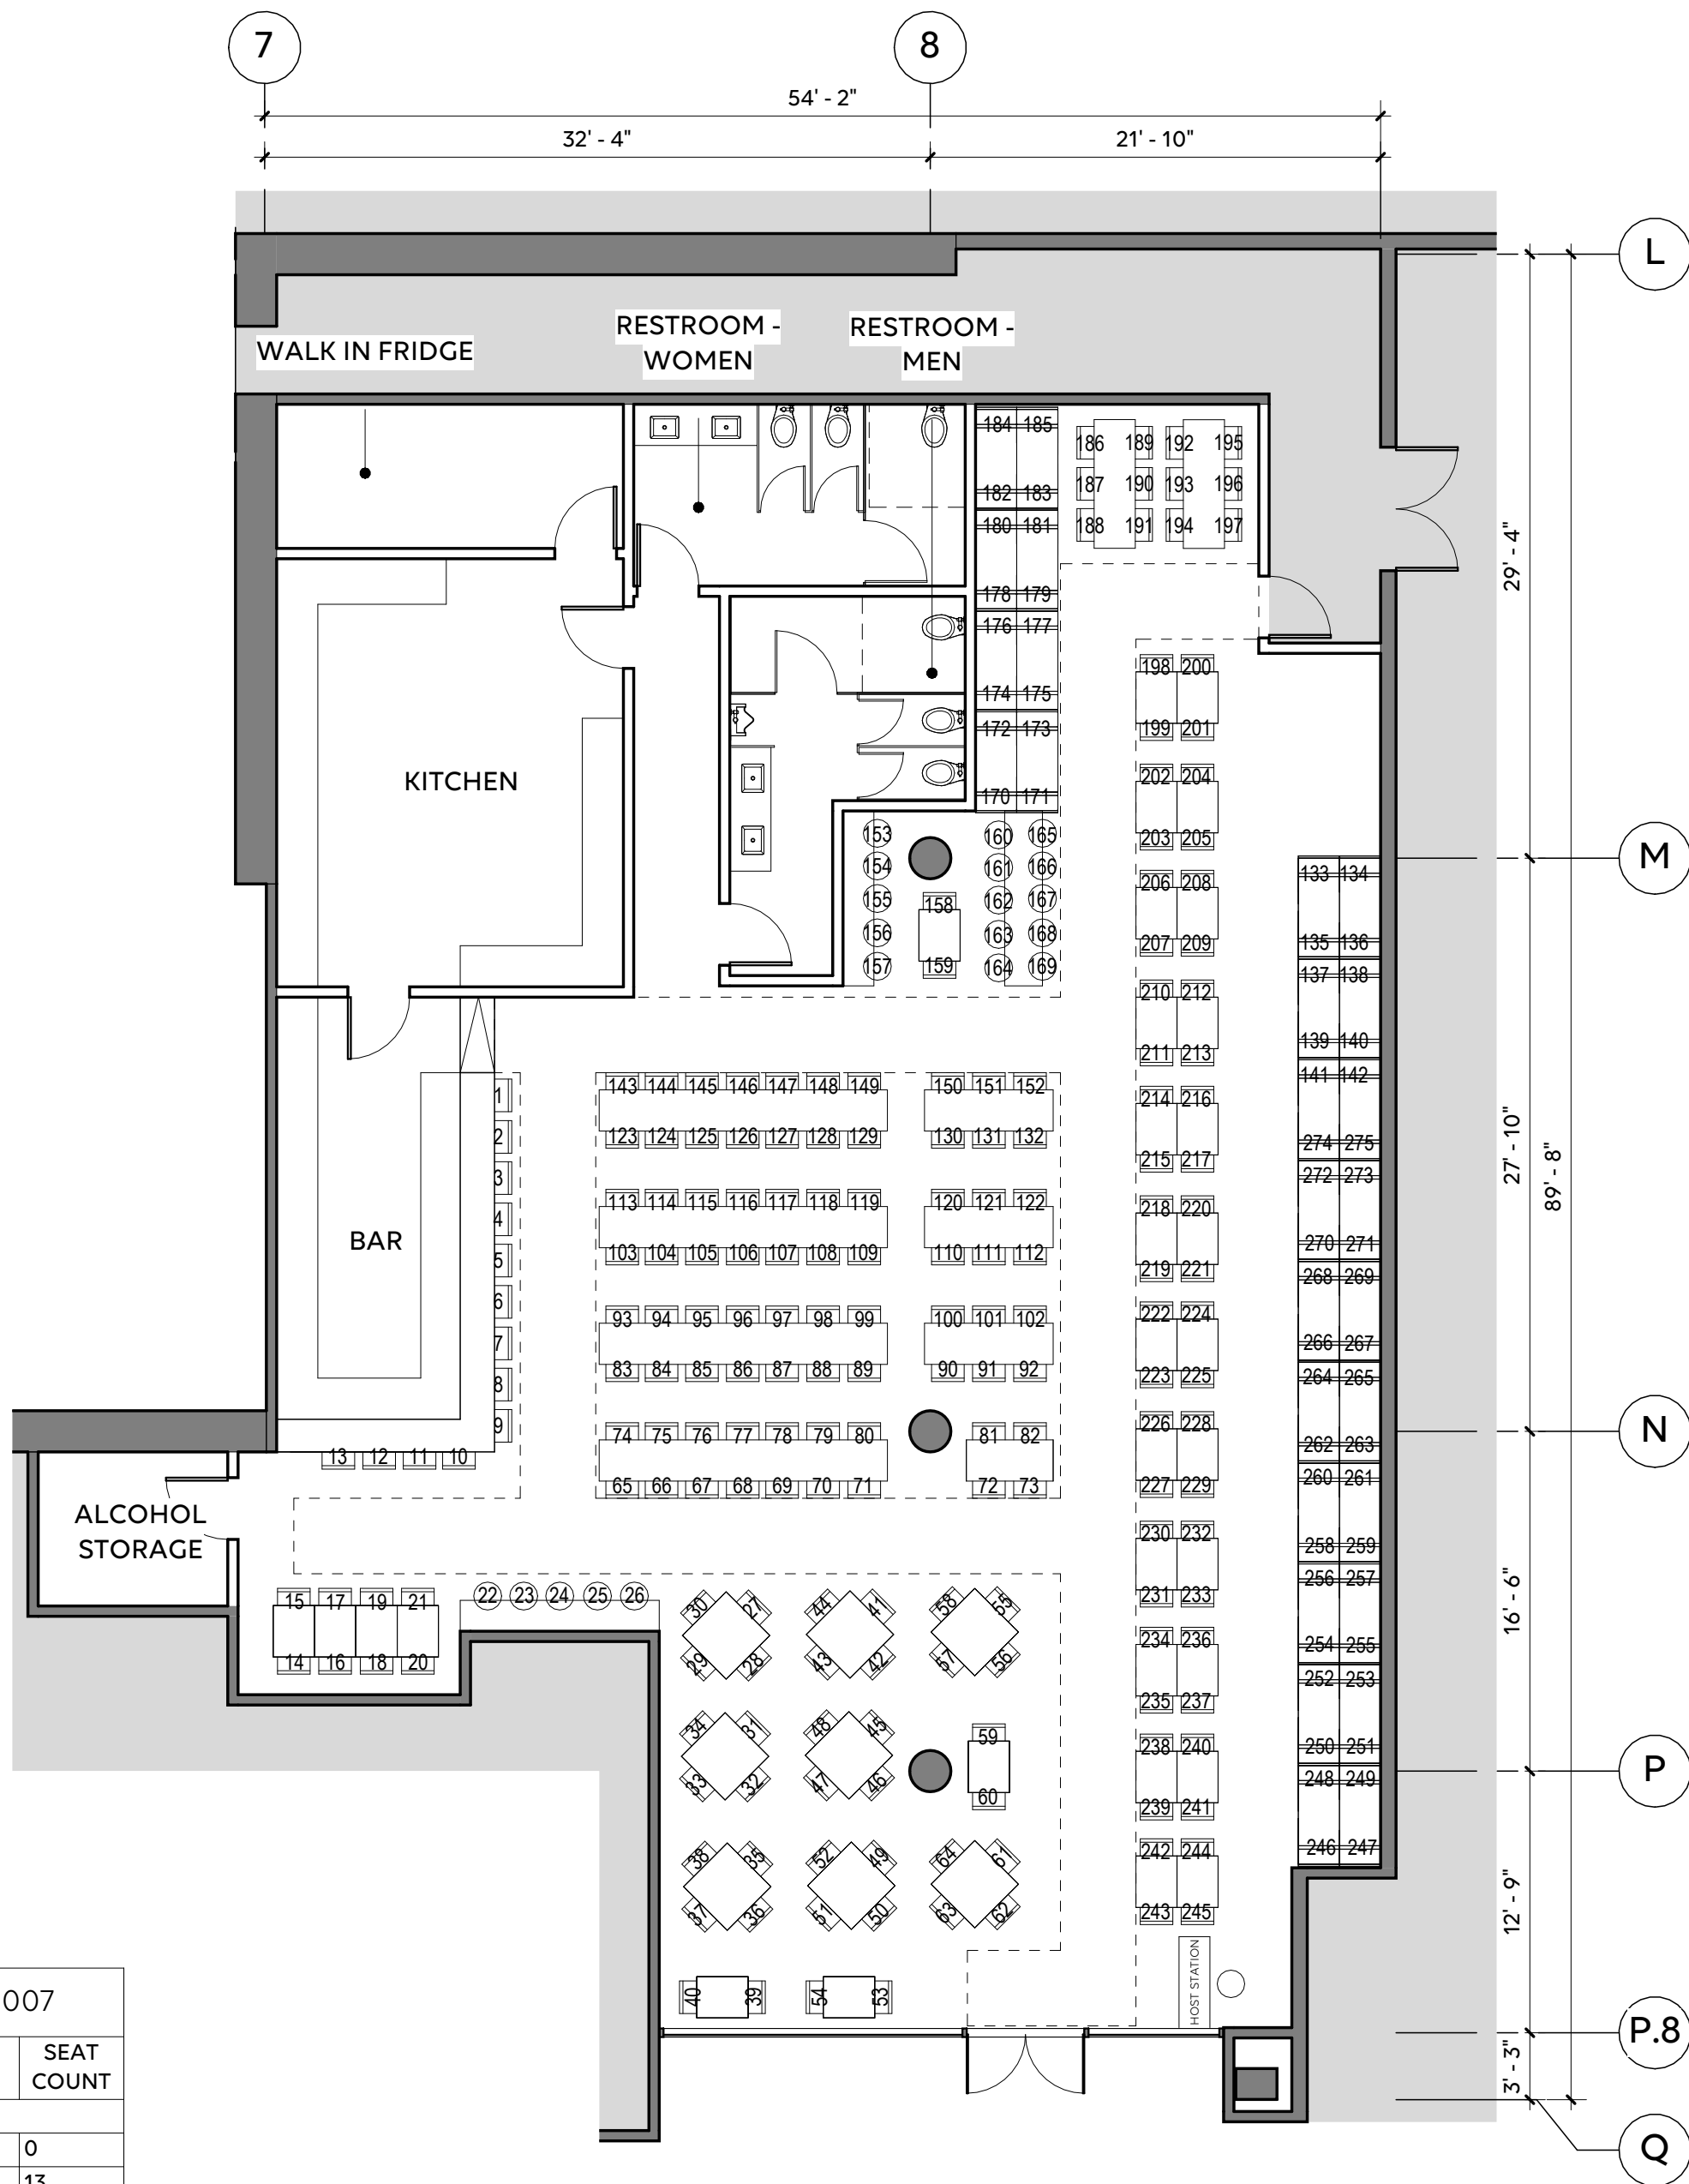

BEER AND WINE RESTAURANT- 007
1/8" = 1'-0"

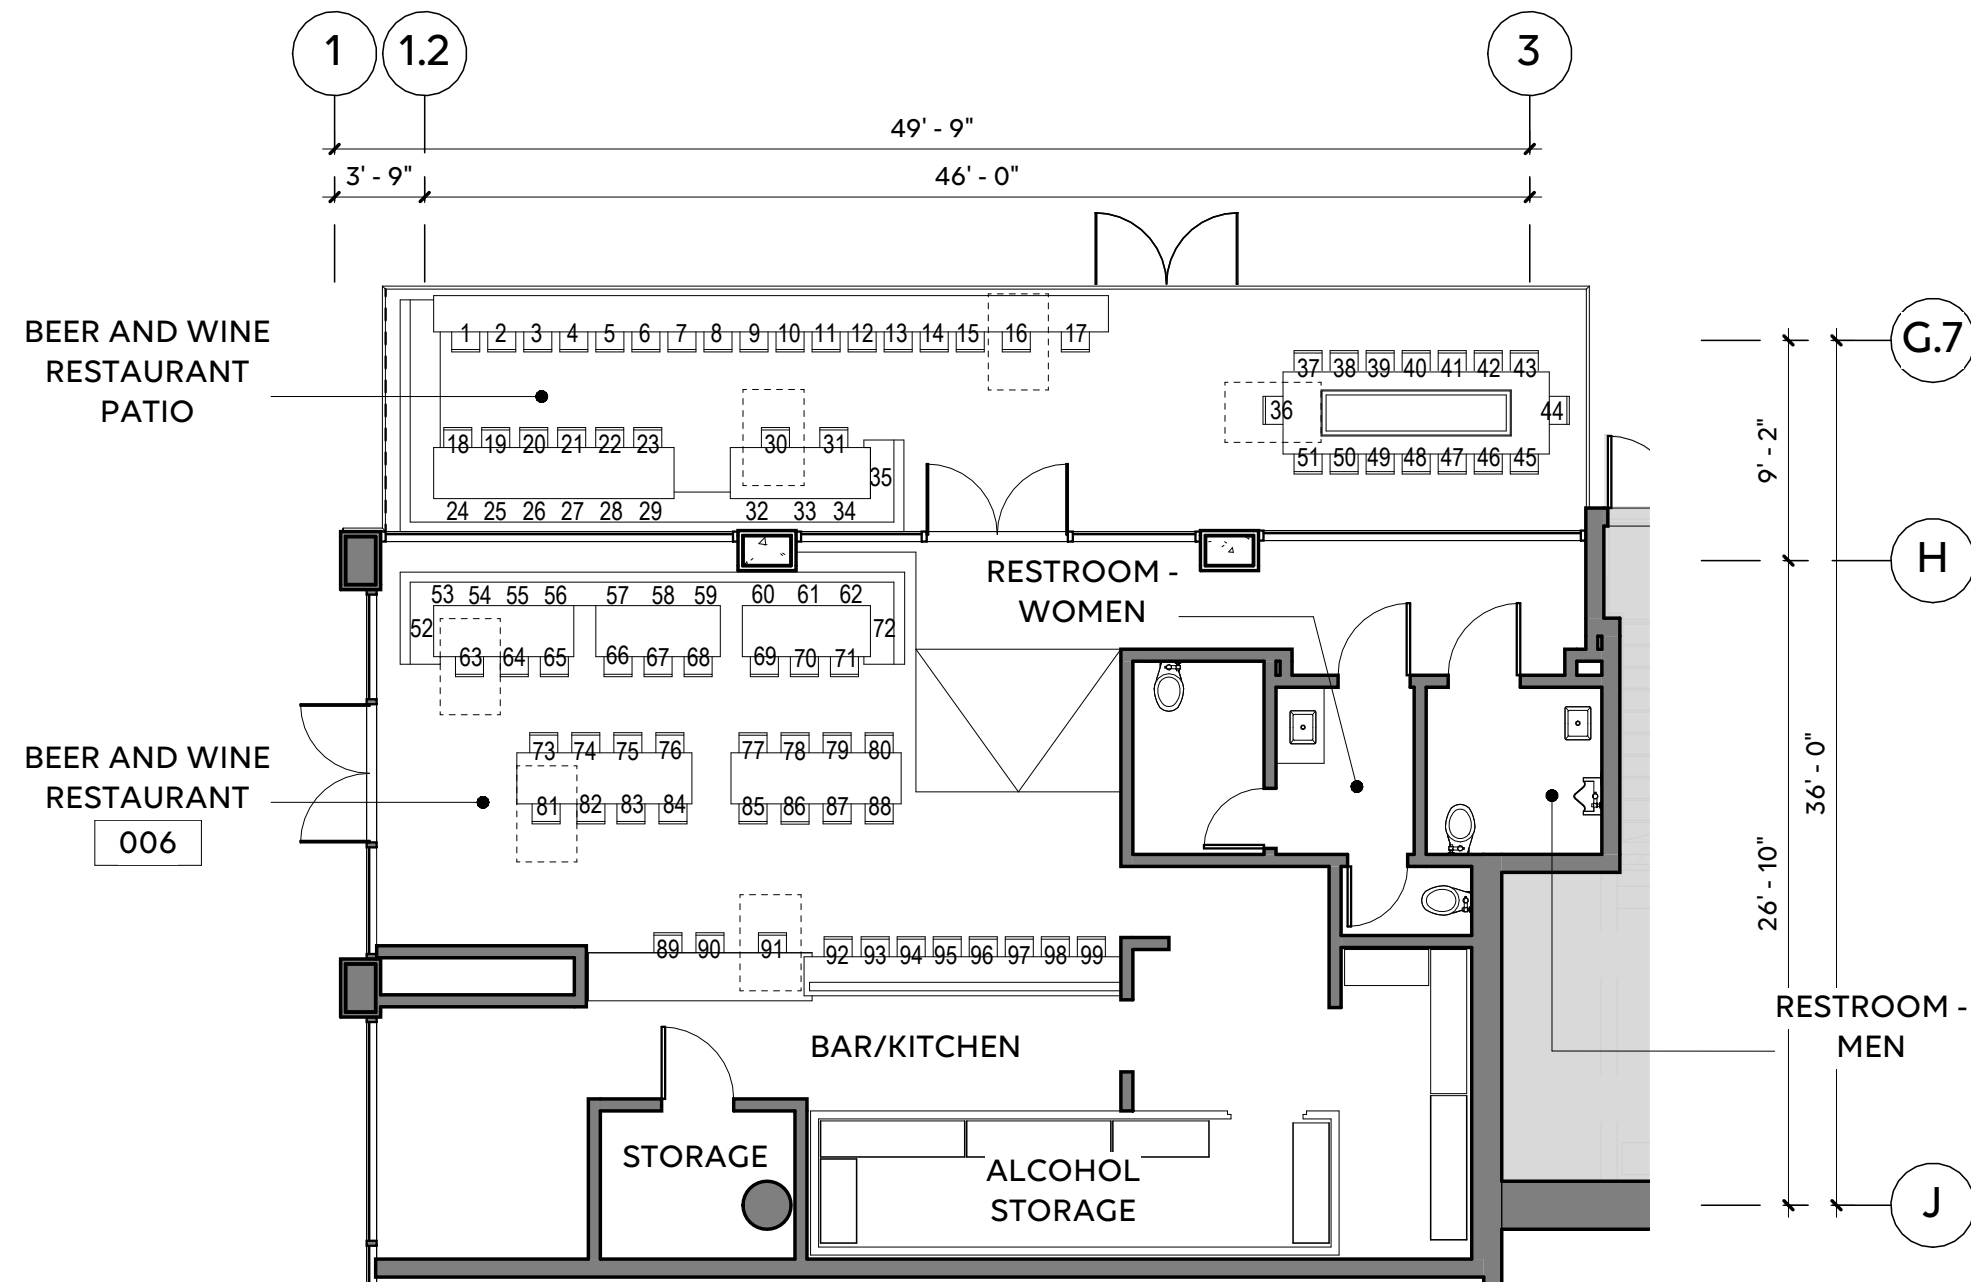

BEER AND WINE RESTAURNT - 006
1/8" = 1'-0"

LEGEND

- WALL
- AREA NOT A PART
- (E) TENANT NOT A PART

OMGIVNING
architecture / interiors

1301 N. BROADWAY
LOS ANGELES, CA 90012

EL CENTRO
6200 HOLLYWOOD BLVD.
LOS ANGELES, CA 90028

CUP/CUB PLAN

REVISIONS:

08.05.24

CUP/CUB PLAN



A-13

8/5/2024 8:05:18 PM

THIS DRAWING AND THE INFORMATION CONTAINED HEREIN ARE THE COPYRIGHTED WORK OF OMGIVNING ARCHITECTS AND MAY NOT BE REPRODUCED WITHOUT WRITTEN PERMISSION.

Plans Approved
as required by
City Los Angeles
Zoning Administrator
ZA-2017-5013-MCUP
Case No.
Ricardo Martinez
Signature
09/17/2024
Date

MARKET - 009		
Name	Area	SEAT COUNT
BACK OF HOUSE	450 SF	0
BEVERAGE AND ALCOHOL STORAGE	321 SF	0
CHECKOUT/SALES	919 SF	0
GENERAL STOCK	832 SF	0
MARKET	3092 SF	0
OFFICE	108 SF	0
RESTROOM - WOMEN	93 SF	0
RESTROOM MEN	93 SF	0
WALK IN COOLER	599 SF	0
Grand total	6508 SF	0

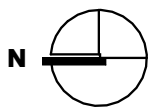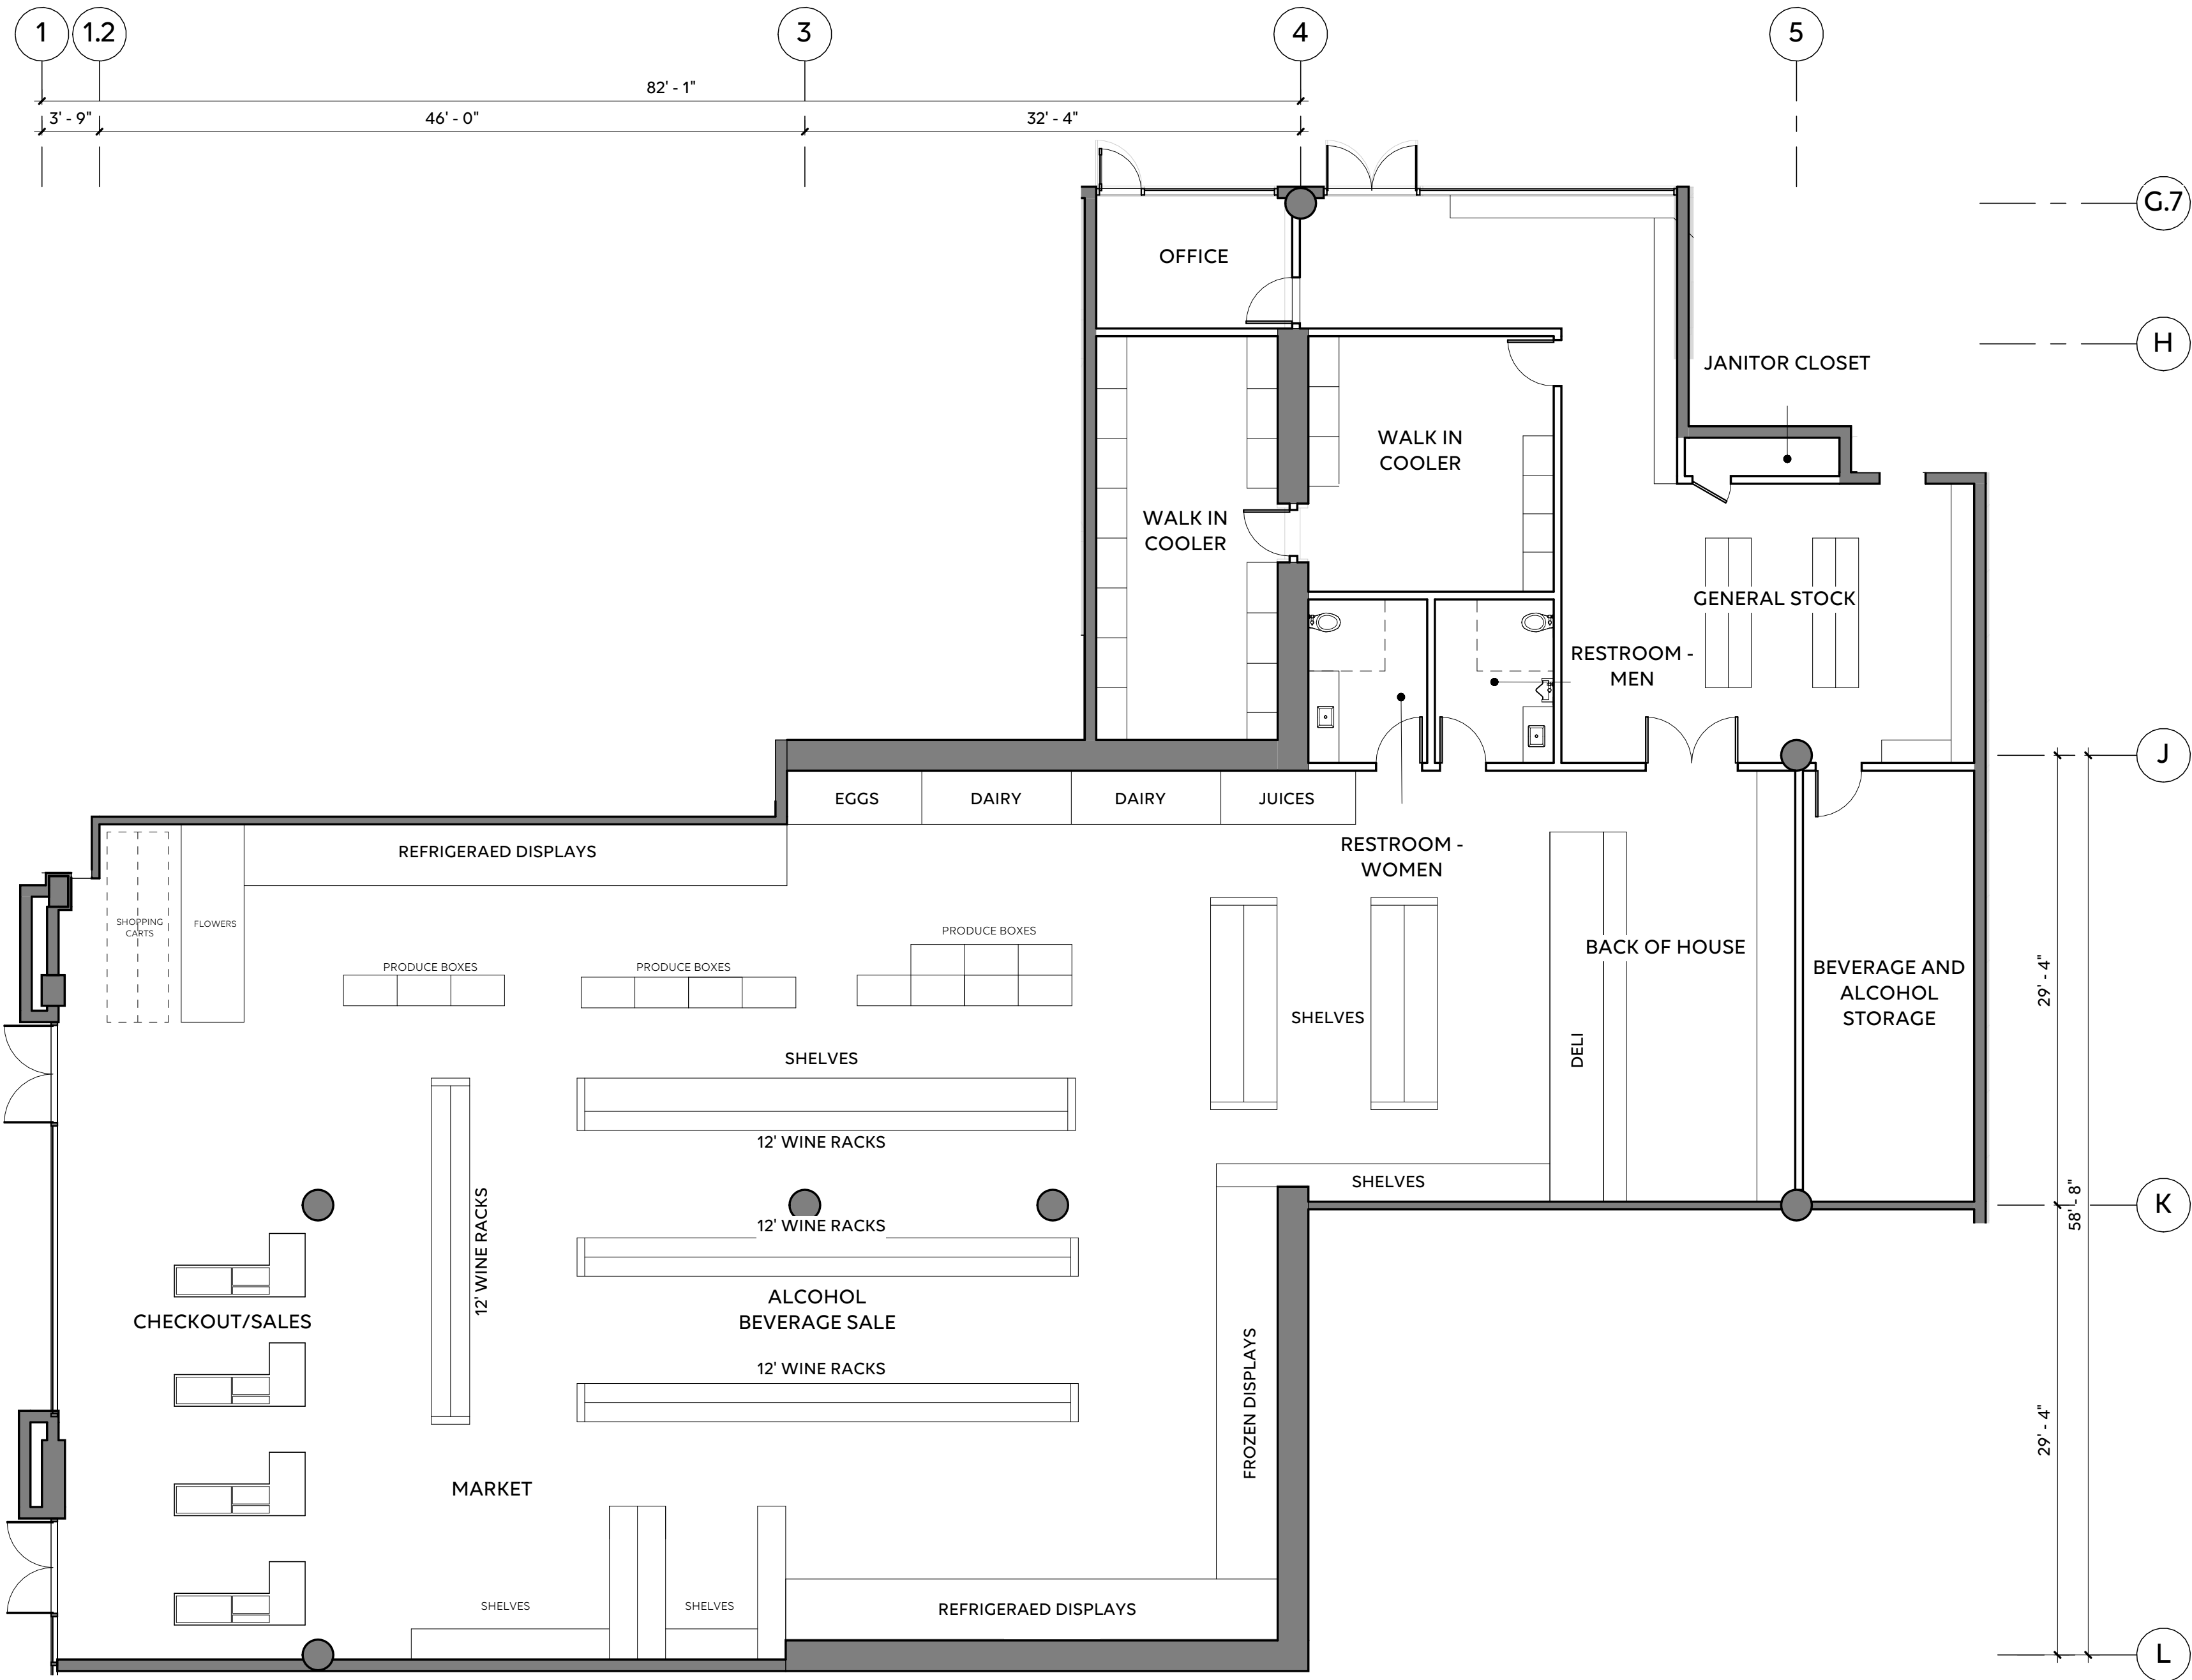

MARKET - 009
1/8" = 1'-0"

1

LEGEND

- WALL
- AREA NOT A PART
- (E) TENANT NOT A PART

OMGIVNING
architecture / interiors

1301 N. BROADWAY
LOS ANGELES, CA 90012

EL CENTRO
6200 HOLLYWOOD BLVD.
LOS ANGELES, CA 90028

CUP/CUB PLAN

REVISIONS:

08.05.24

CUP/CUB PLAN

A-14